




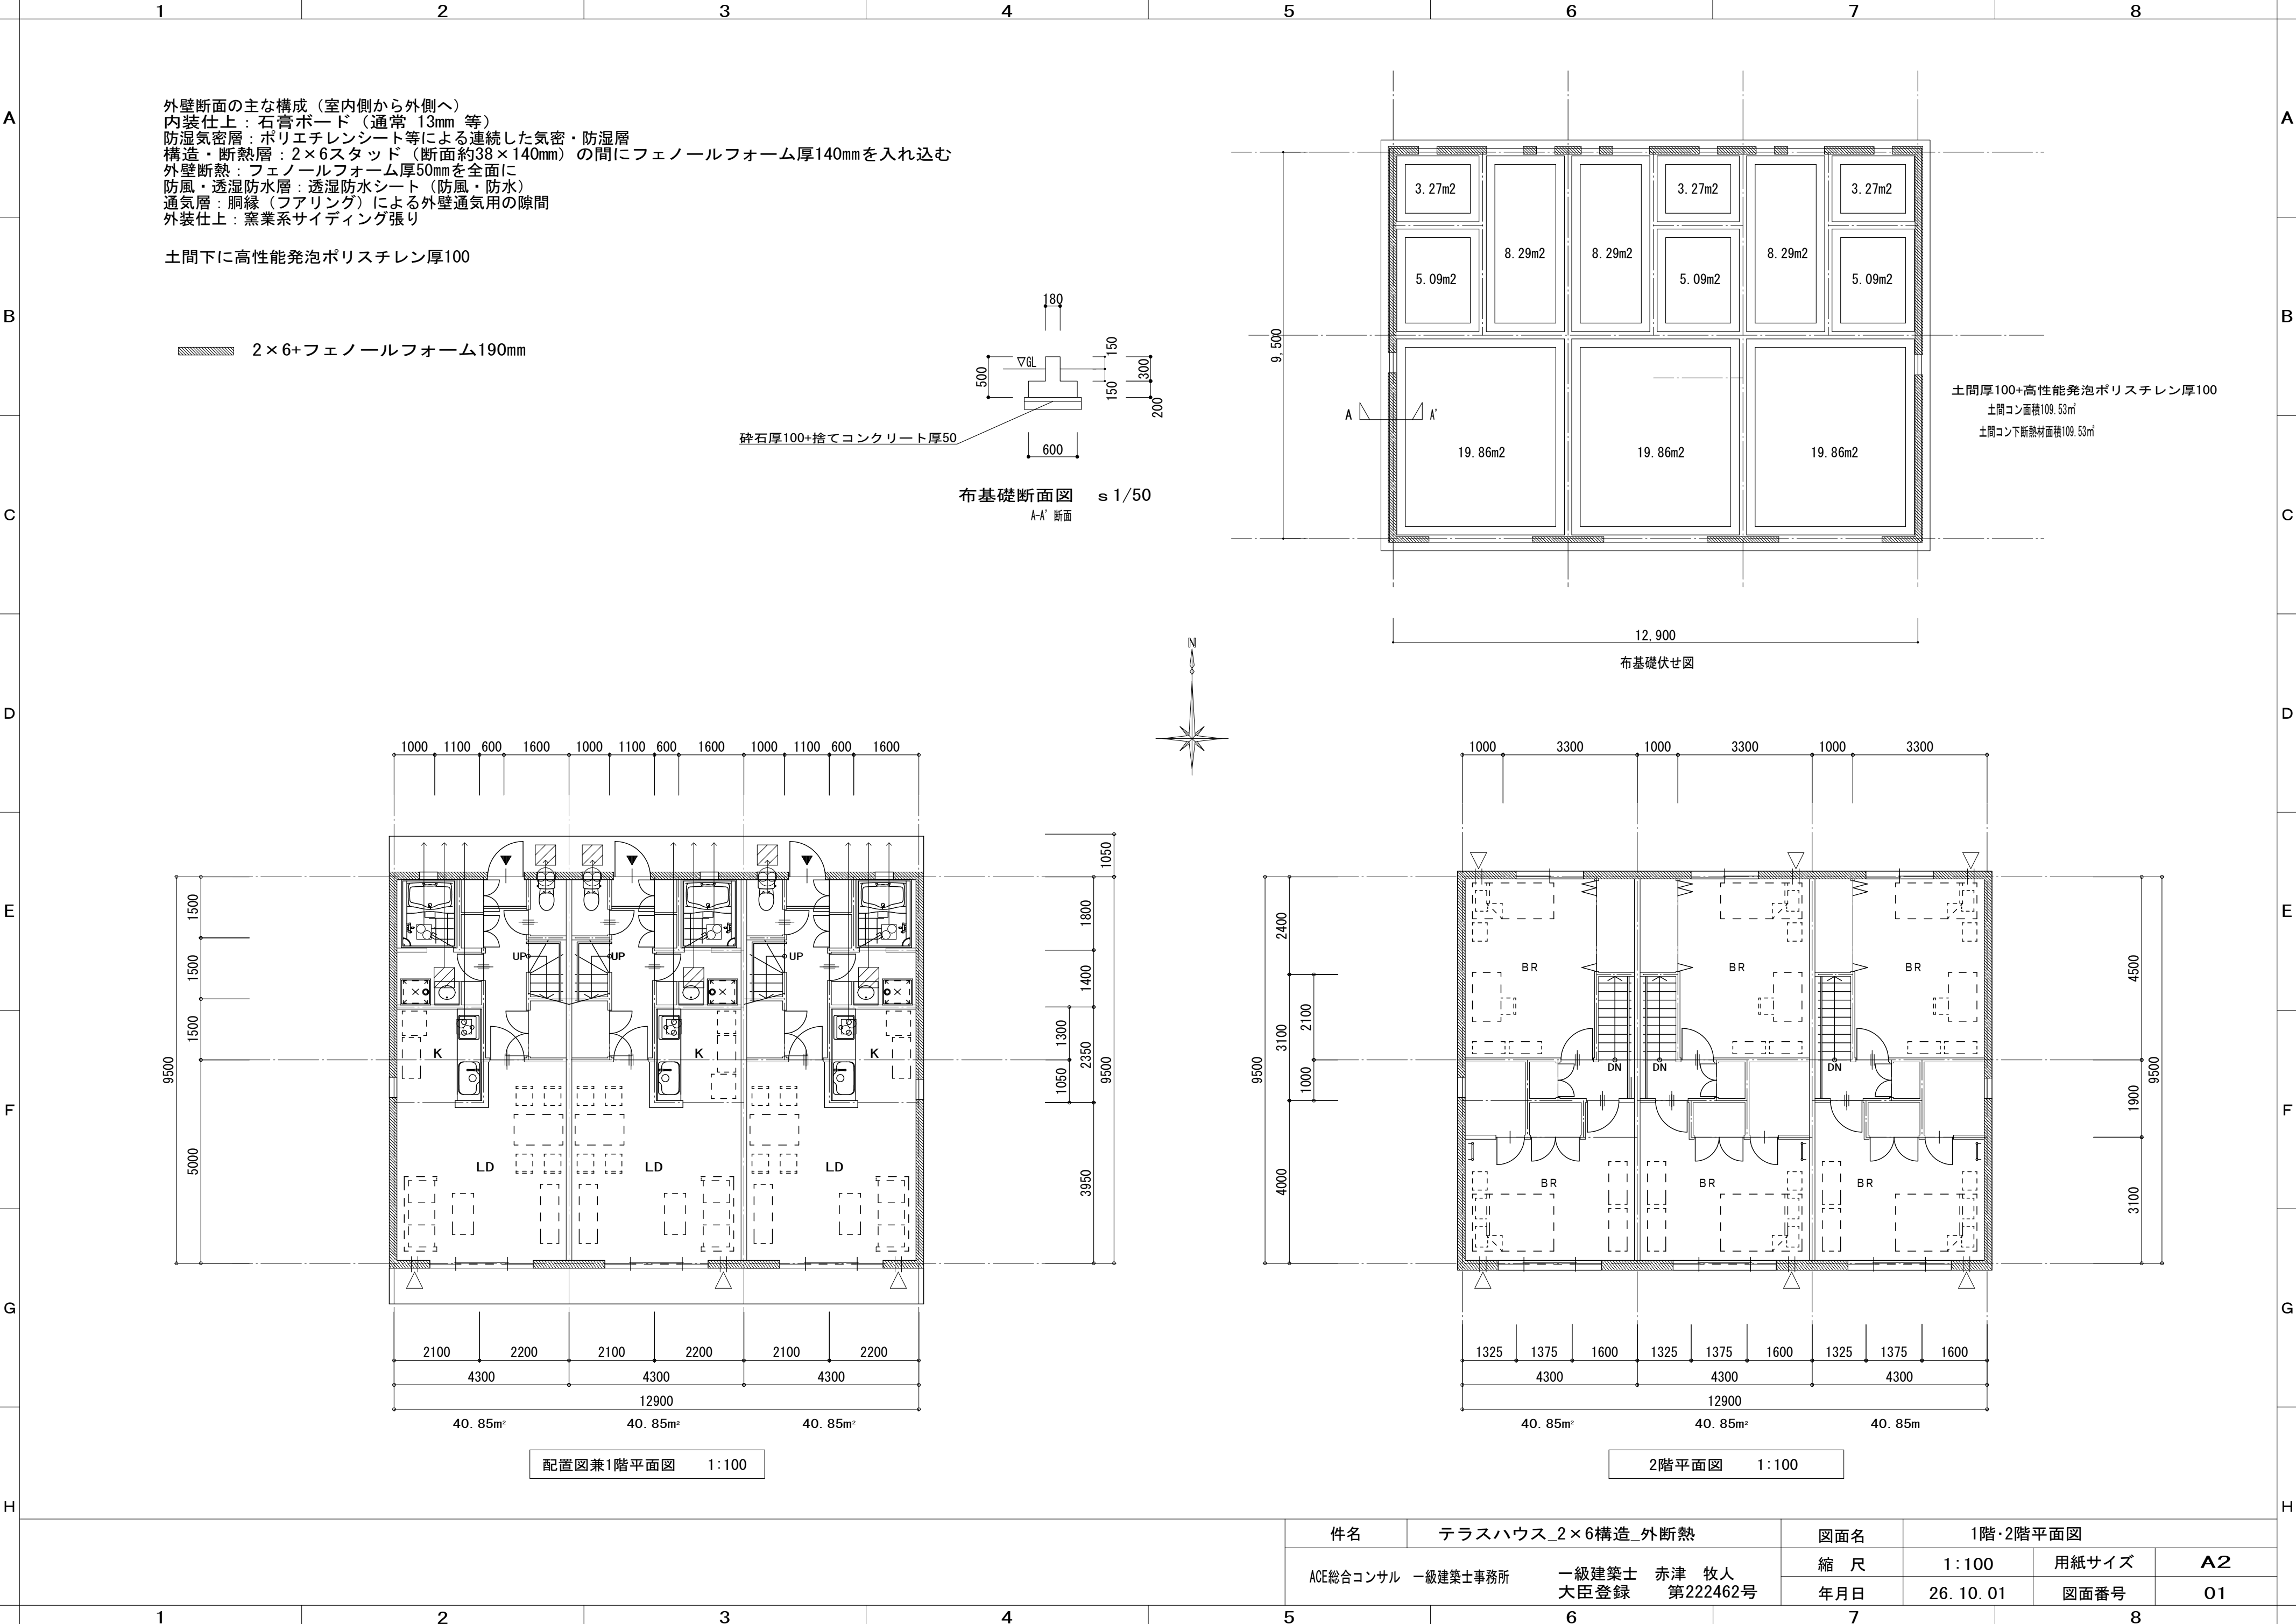

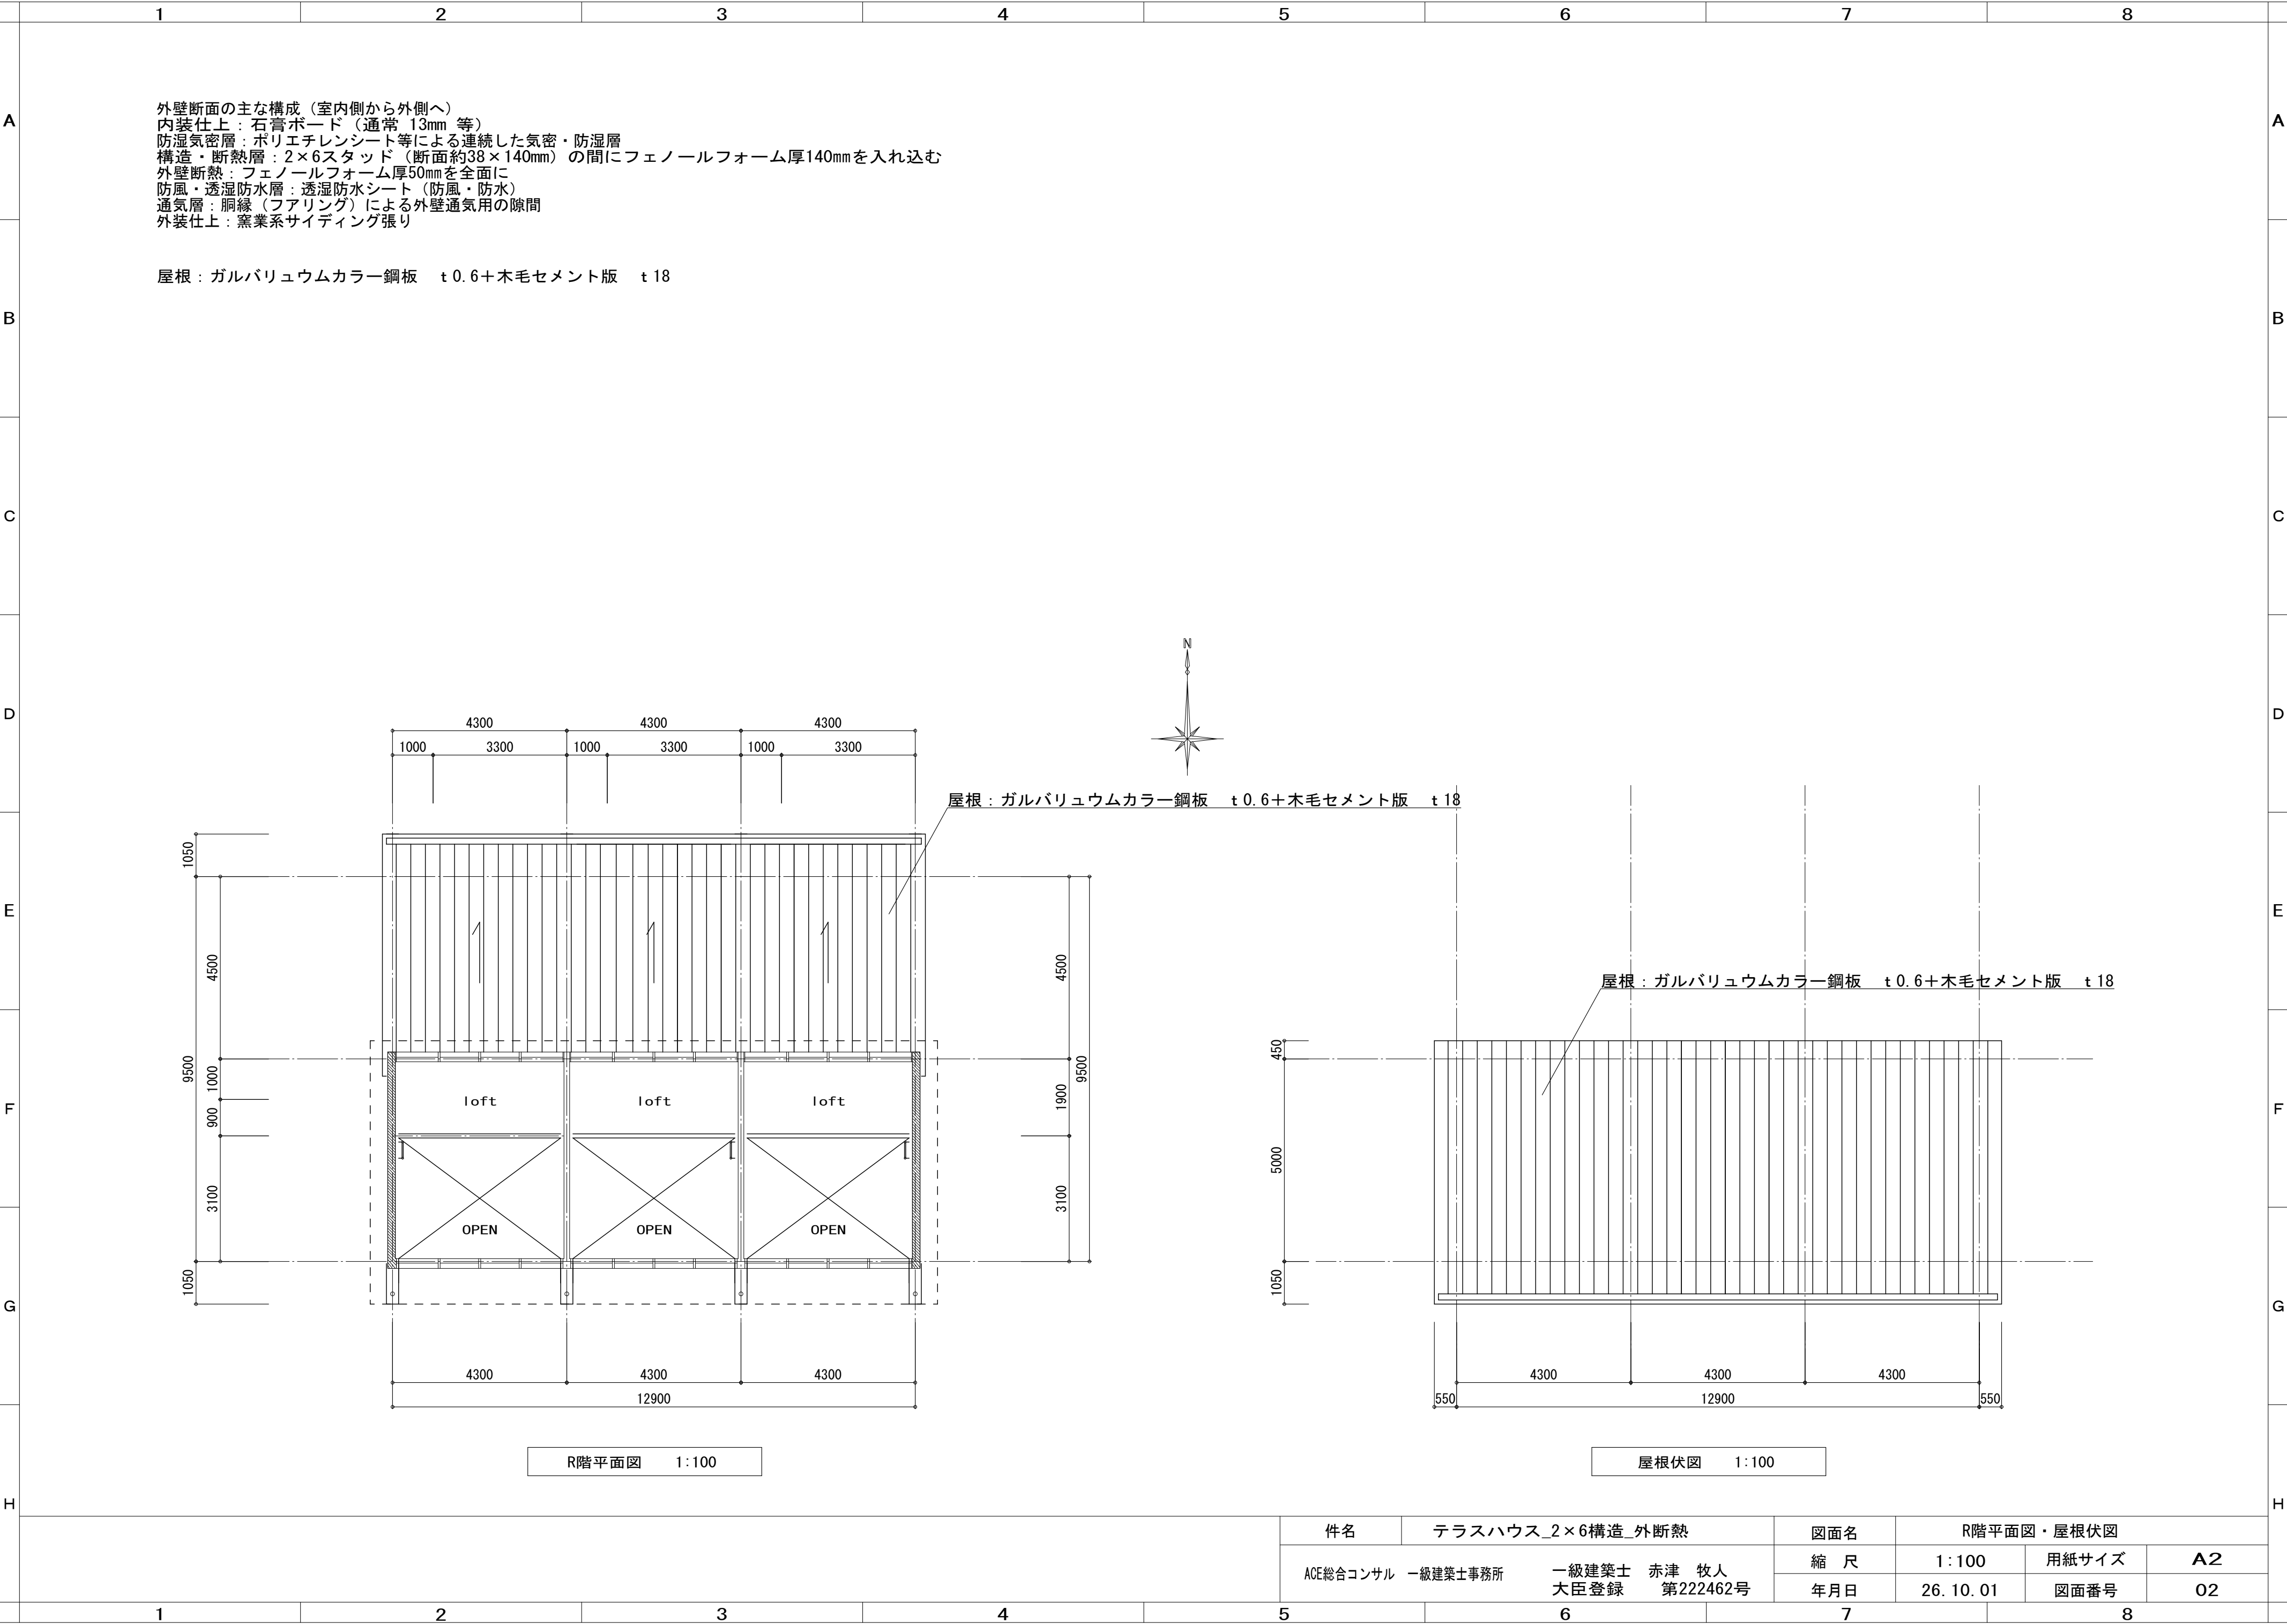

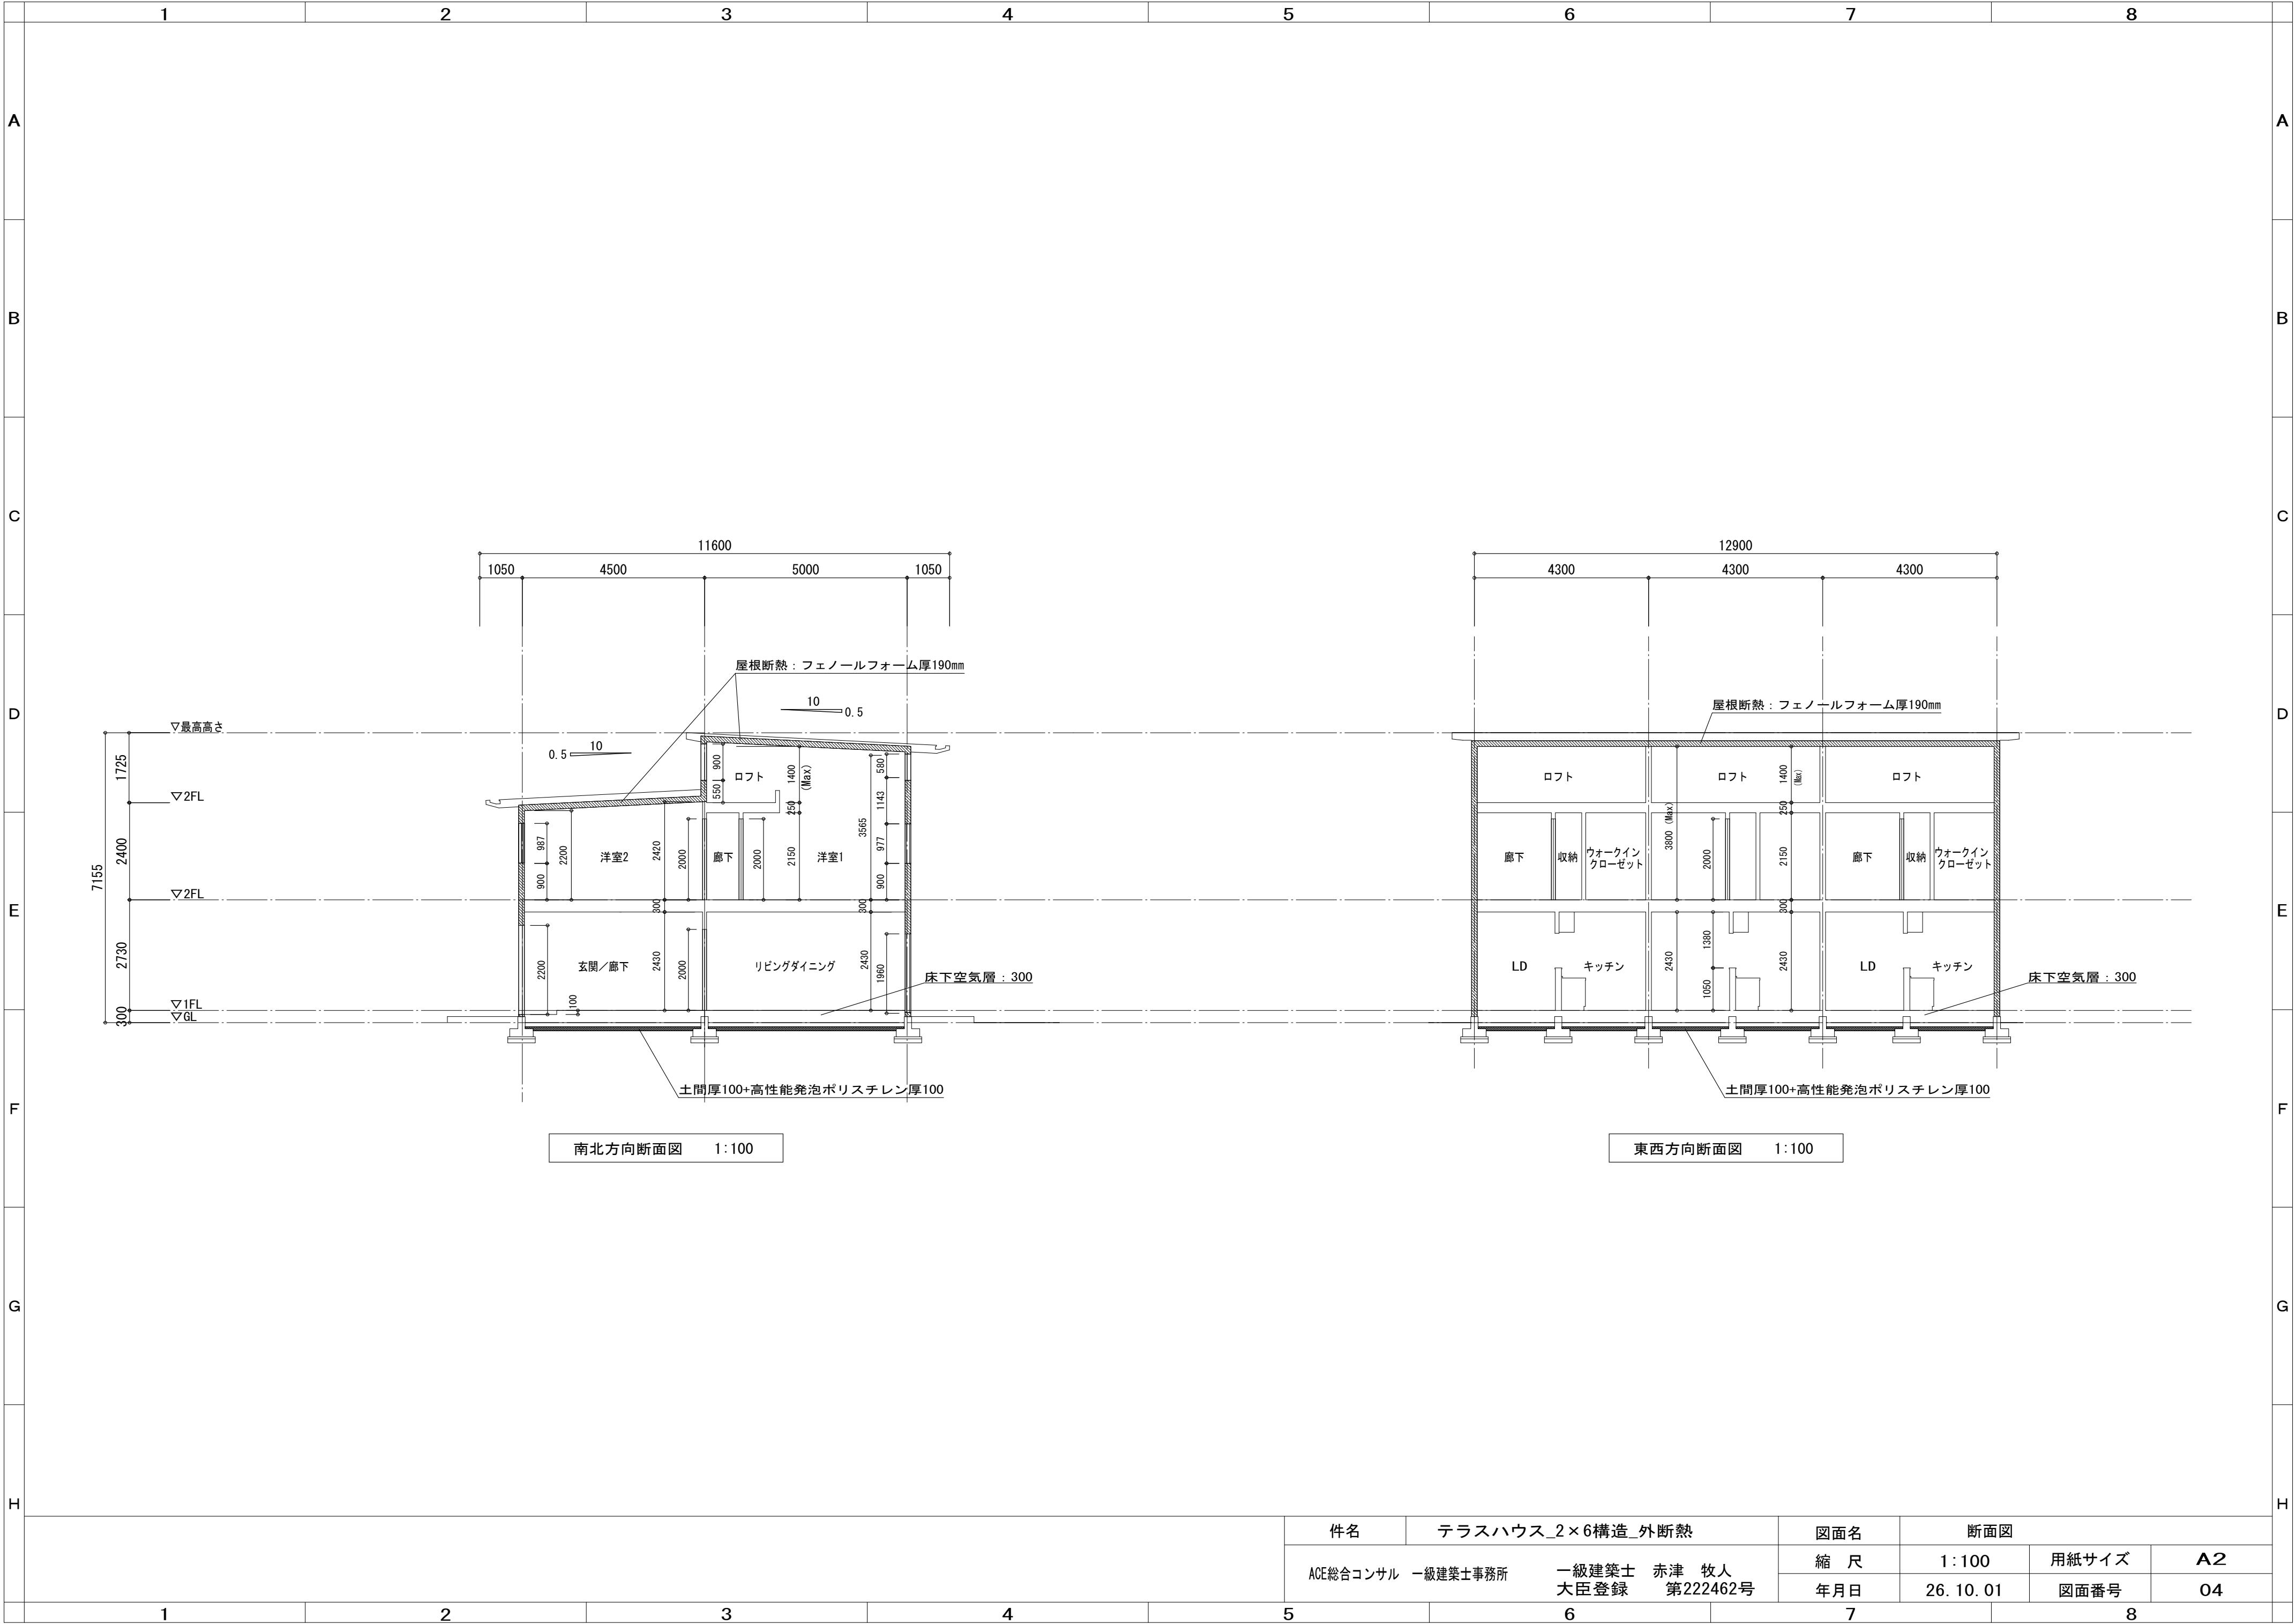

ACE総合コンサル 一級建築士事務所 一級建築士 赤津 牧人 大臣登録 第222462号	件名	テラスハウス_2×6構造_外断熱		図面名	断面図		
	縮尺	1:100		年月日	26. 10. 01	用紙サイズ	A2
	図面番号	04					

