

外壁断面上の主な構成（室内側から外側へ）  
 内装仕上：石膏ボード（通常 13mm 等）  
 防湿気密層：ポリエチレンシート等による連続した気密・防湿層  
 構造 RC300mm  
 外断熱層：フェノールフォーム厚150mm  
 外装下地：ポリマーセメント+ガラス繊維メッシュ  
 仕上げ塗材：フッ素塗料塗装


外壁断面の主な構成（室内側から外側へ）  
 内装仕上：石膏ボード（通常 13mm 等）  
 防湿気密層：ポリエチレンシート等による連続した気密・防湿層  
 構造：2×6  
 外断熱層：フェノールフォーム厚140mm+60mm＝200mm  
 外装下地：ポリマーセメント+ガラス繊維メッシュ  
 仕上げ塗材：フッ素塗料塗装

RC



 C B 120mm

 2×6+フェノールフォーム

フェノールフォーム

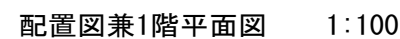

※宅地の切盛土なし

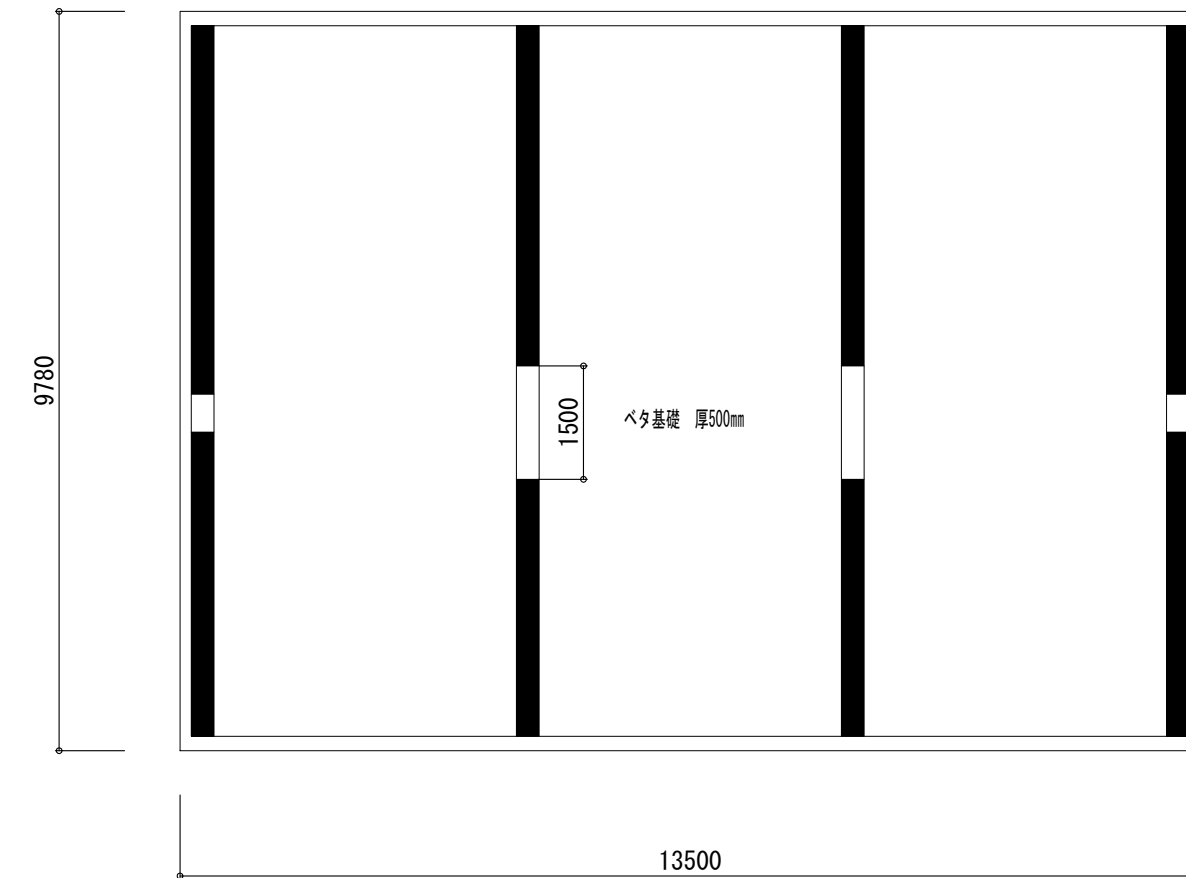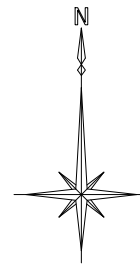
天井と床面積：37.60m<sup>2</sup>/戸　3戸：112.8m<sup>2</sup>

天井と床面積：37.60m<sup>2</sup>/戸 3戸：112.8m<sup>2</sup>


|                    |                              |     |            |       |    |
|--------------------|------------------------------|-----|------------|-------|----|
| 件名                 | テラスハウス_AZRAS構造_外断熱           | 図面名 | 1階・2階平面図   |       |    |
| ACE総合コンサル 一級建築士事務所 | 一級建築士 赤津 牧人<br>大臣登録 第222462号 | 縮 尺 | 1:100      | 用紙サイズ | A2 |
|                    |                              | 年月日 | 26. 10. 01 | 図面番号  | 01 |

外壁断面上の主な構成（室内側から外側へ）  
 内装仕上：石膏ボード（通常 13mm 等）  
 防湿気密層：ポリエチレンシート等による連続した気密・防湿層  
 構造：RC300mm  
 外断熱層：フェノールフォーム厚150mm  
 外装下地：ポリマーセメント+ガラス繊維メッシュ  
 仕上げ塗材：フッ素塗料塗装


外壁断面の主な構成（室内側から外側へ）  
 内装仕上：石膏ボード（通常 13mm 等）  
 防湿気密層：ポリエチレンシート等による連続した気密・防湿層  
 構造：2×6  
 外断熱層：フェノールフォーム厚140mm+60mm＝200mm  
 外装下地：ポリマーセメント＋ガラス繊維メッシュ  
 仕上げ塗材：フッ素塗料塗装

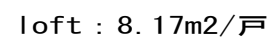

R階平面図 1:100

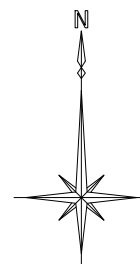


屋根：ガルバリウムカラー鋼板 t 0.6+木毛セメント版 t 18

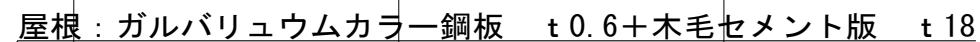


屋根伏図 1:100

|                    |                              |     |            |       |            |  |  |
|--------------------|------------------------------|-----|------------|-------|------------|--|--|
| 件名                 | テラスハウス_AZRAS構造_外断熱           |     |            | 図面名   | R階平面図・屋根伏図 |  |  |
| ACE総合コンサル 一級建築士事務所 | 一級建築士 赤津 牧人<br>大臣登録 第222462号 | 縮 尺 | 1:100      | 用紙サイズ | A2         |  |  |
|                    |                              | 年月日 | 26. 10. 01 | 図面番号  | 02         |  |  |

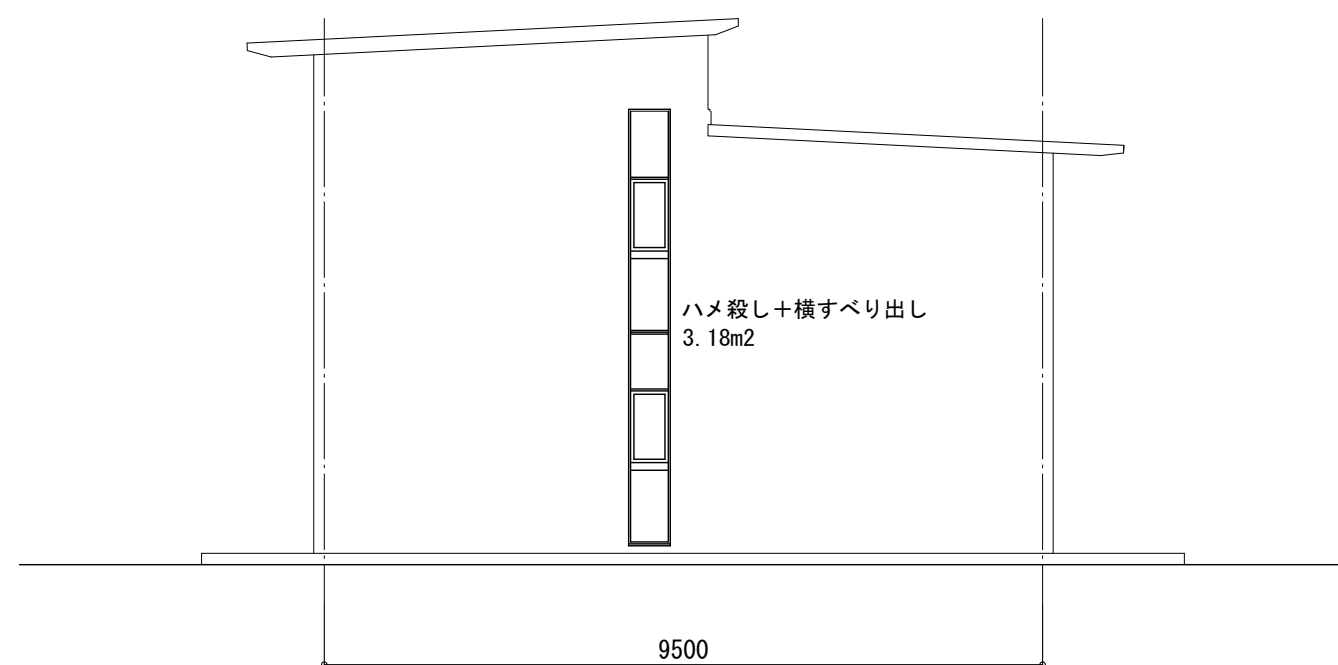

東立面図 1:100


東面RC外壁：面積 $59.76\text{m}^2 - 3.18\text{m}^2 = 56.58\text{m}^2$

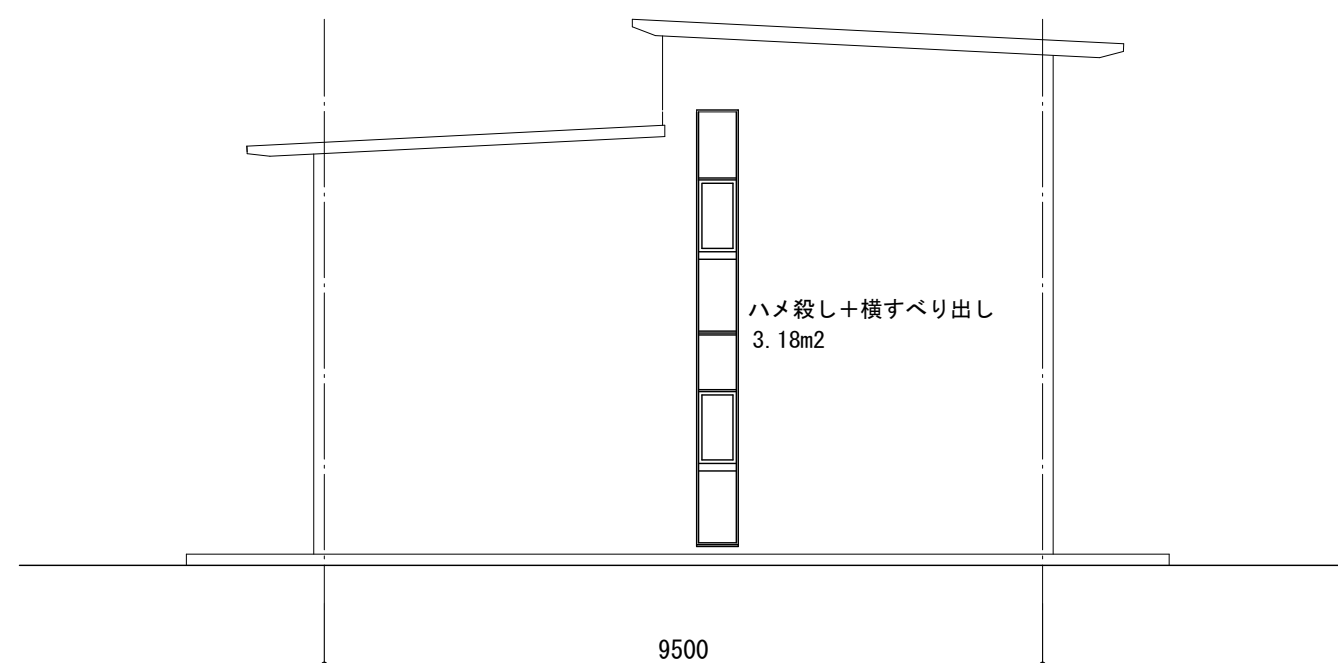

西立面图 1:100

西面RC外壁：面積 $59.76\text{m}^2 - 3.18\text{m}^2 = 56.58\text{m}^2$

西面+東面RC外壁：面積合計 113.16m<sup>2</sup>

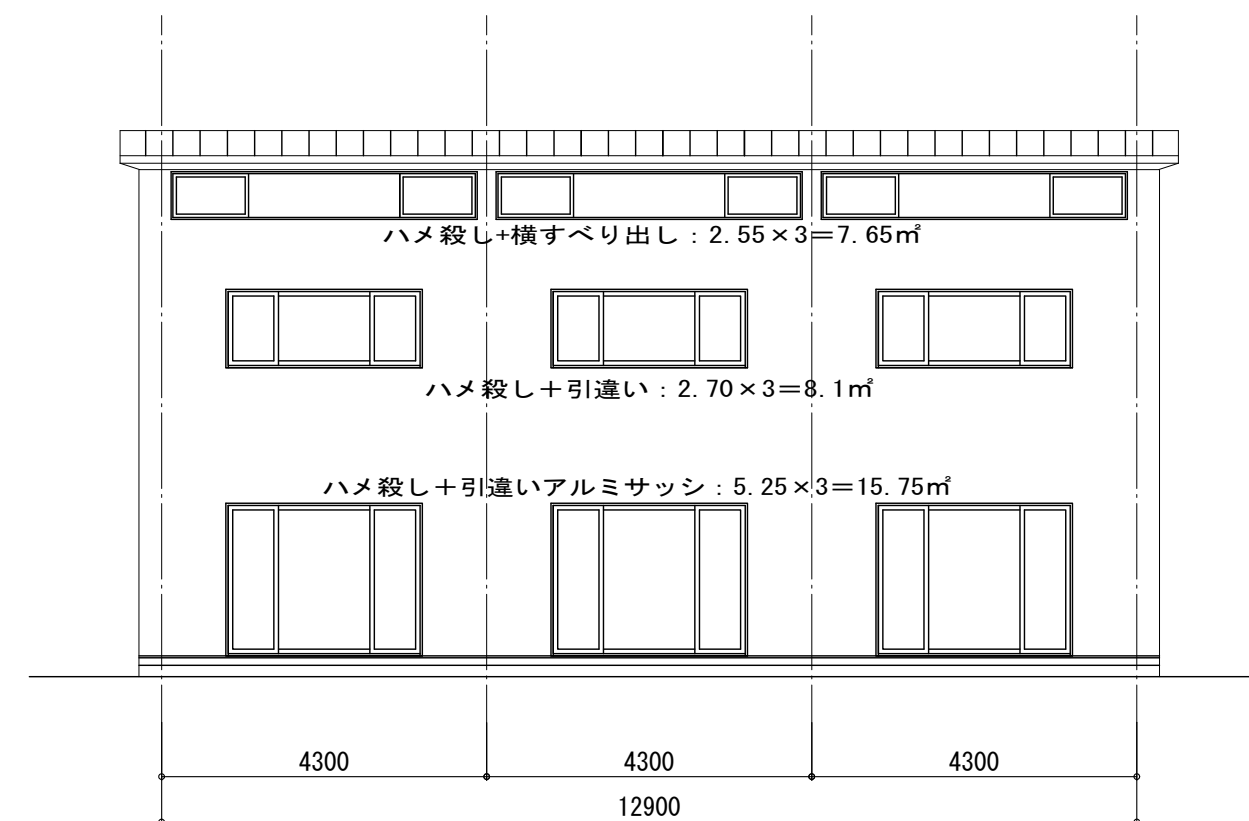


ハメ殺し+引違い： $2.70 \times 3 = 8.1\text{m}^2$

ハメ殺し+引違いアルミサッシ :  $5.25 \times 3 = 15.75\text{m}^2$

南立面图 1:100

南面 $2 \times 6$ 外壁：面積 $86.78\text{m}^2 - 31.5\text{m}^2 = 55.28\text{m}^2$

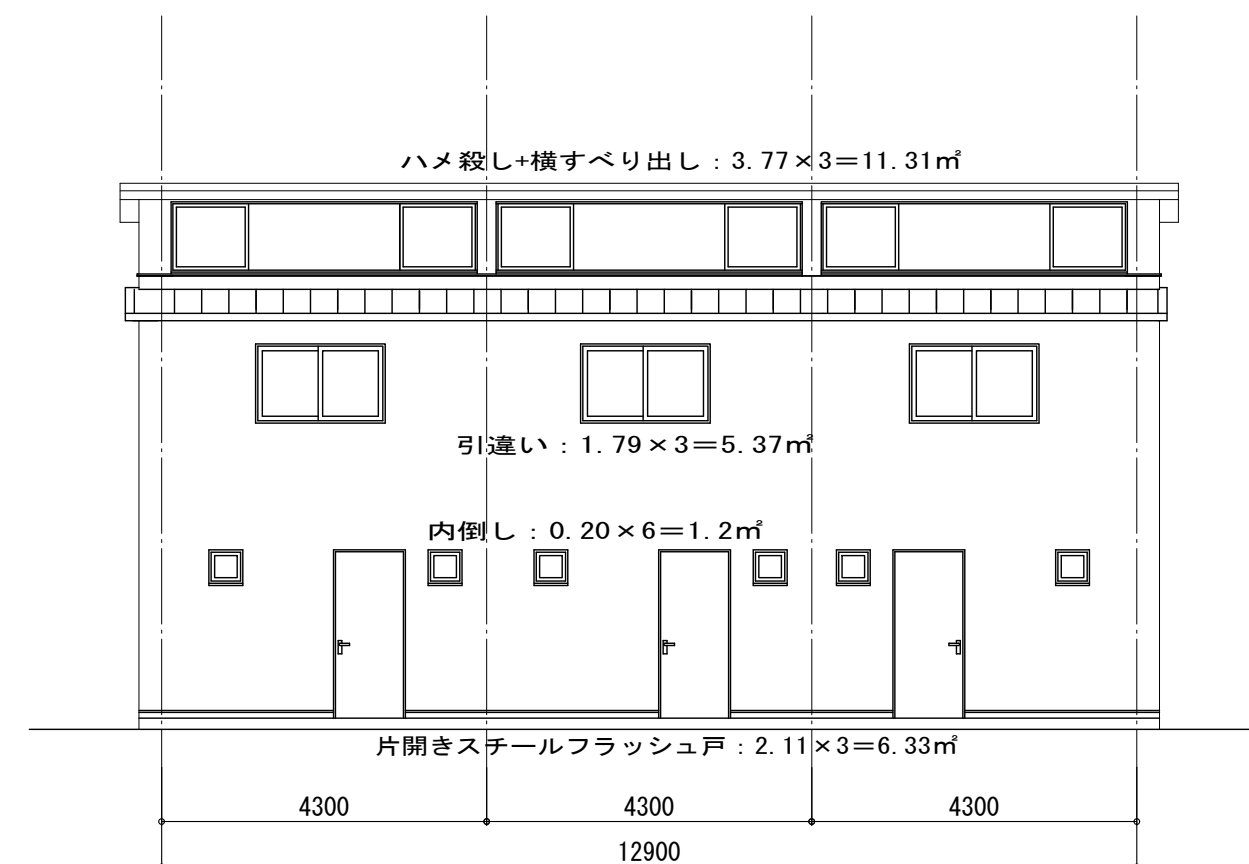

引違い :  $1.79 \times 3 = 5.37\text{m}^2$

内倒し :  $0.20 \times 6 = 1.2\text{m}^2$

片開きスチールフラッシュ戸 :  $2.11 \times 3 = 6.33\text{m}^2$

北立面图 1:100

2×6外壁：13.38m<sup>2</sup>-11.31m<sup>2</sup>=2.07m<sup>2</sup>

2×6外壁：70.03m<sup>2</sup>-12.9m<sup>2</sup>=57.13m<sup>2</sup>


北面2×6外壁合計：59.20m<sup>2</sup>

北面+南面2×6外壁：面積合計 114.48m<sup>2</sup>



高性能トリプルガラス樹脂窓 APW 430


Low-E 3mm+アルゴンガス18mm+フロート 3mm+アルゴンガス18mm+Low-E 3mm

|                    |                              |     |            |       |    |
|--------------------|------------------------------|-----|------------|-------|----|
| 件名                 | テラスハウス_AZRAS構造_外断熱           | 図面名 | 立面図        |       |    |
| ACE総合コンサル 一級建築士事務所 | 一級建築士 赤津 牧人<br>大臣登録 第222462号 | 縮 尺 | 1:100      | 用紙サイズ | A2 |
|                    |                              | 年月日 | 26. 10. 01 | 図面番号  | 03 |

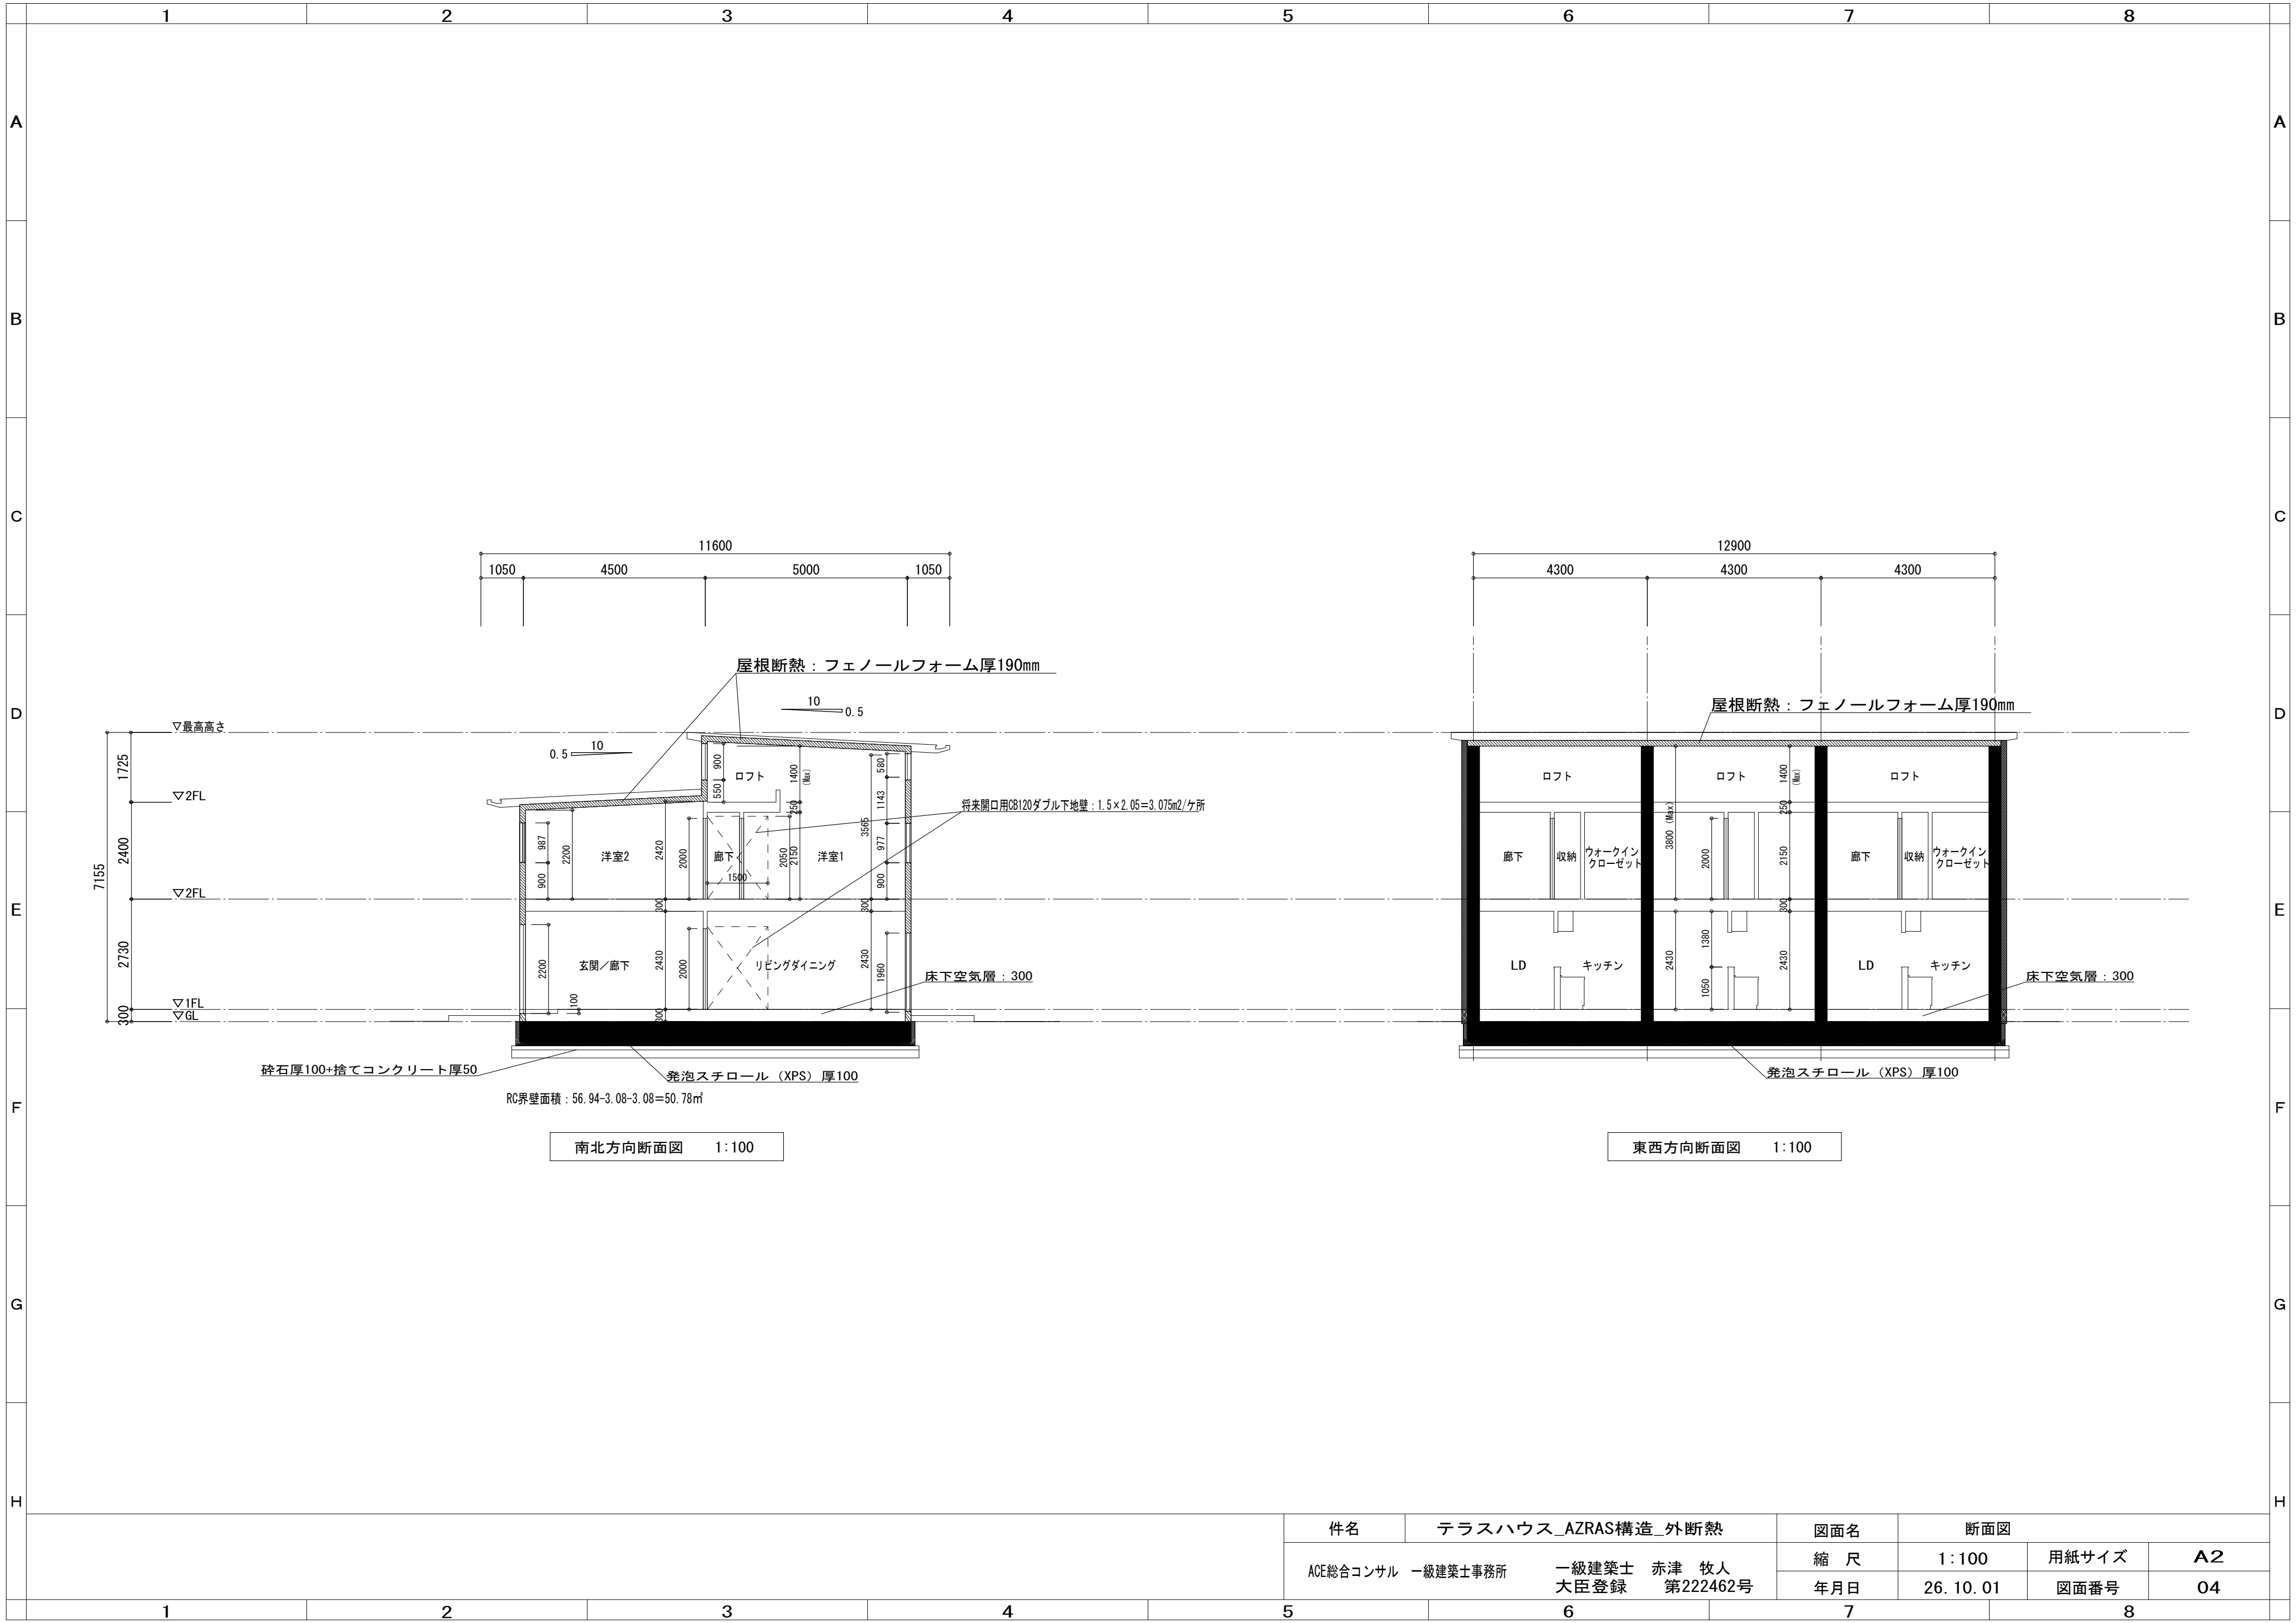

| 件名 | テラスハウス_AZRAS構造_外断熱 | 図面名 |            | 断面図   |    |  |
|----|--------------------|-----|------------|-------|----|--|
|    |                    | 縮 尺 | 1:100      | 用紙サイズ | A2 |  |
|    |                    | 年月日 | 26. 10. 01 | 図面番号  | 04 |  |

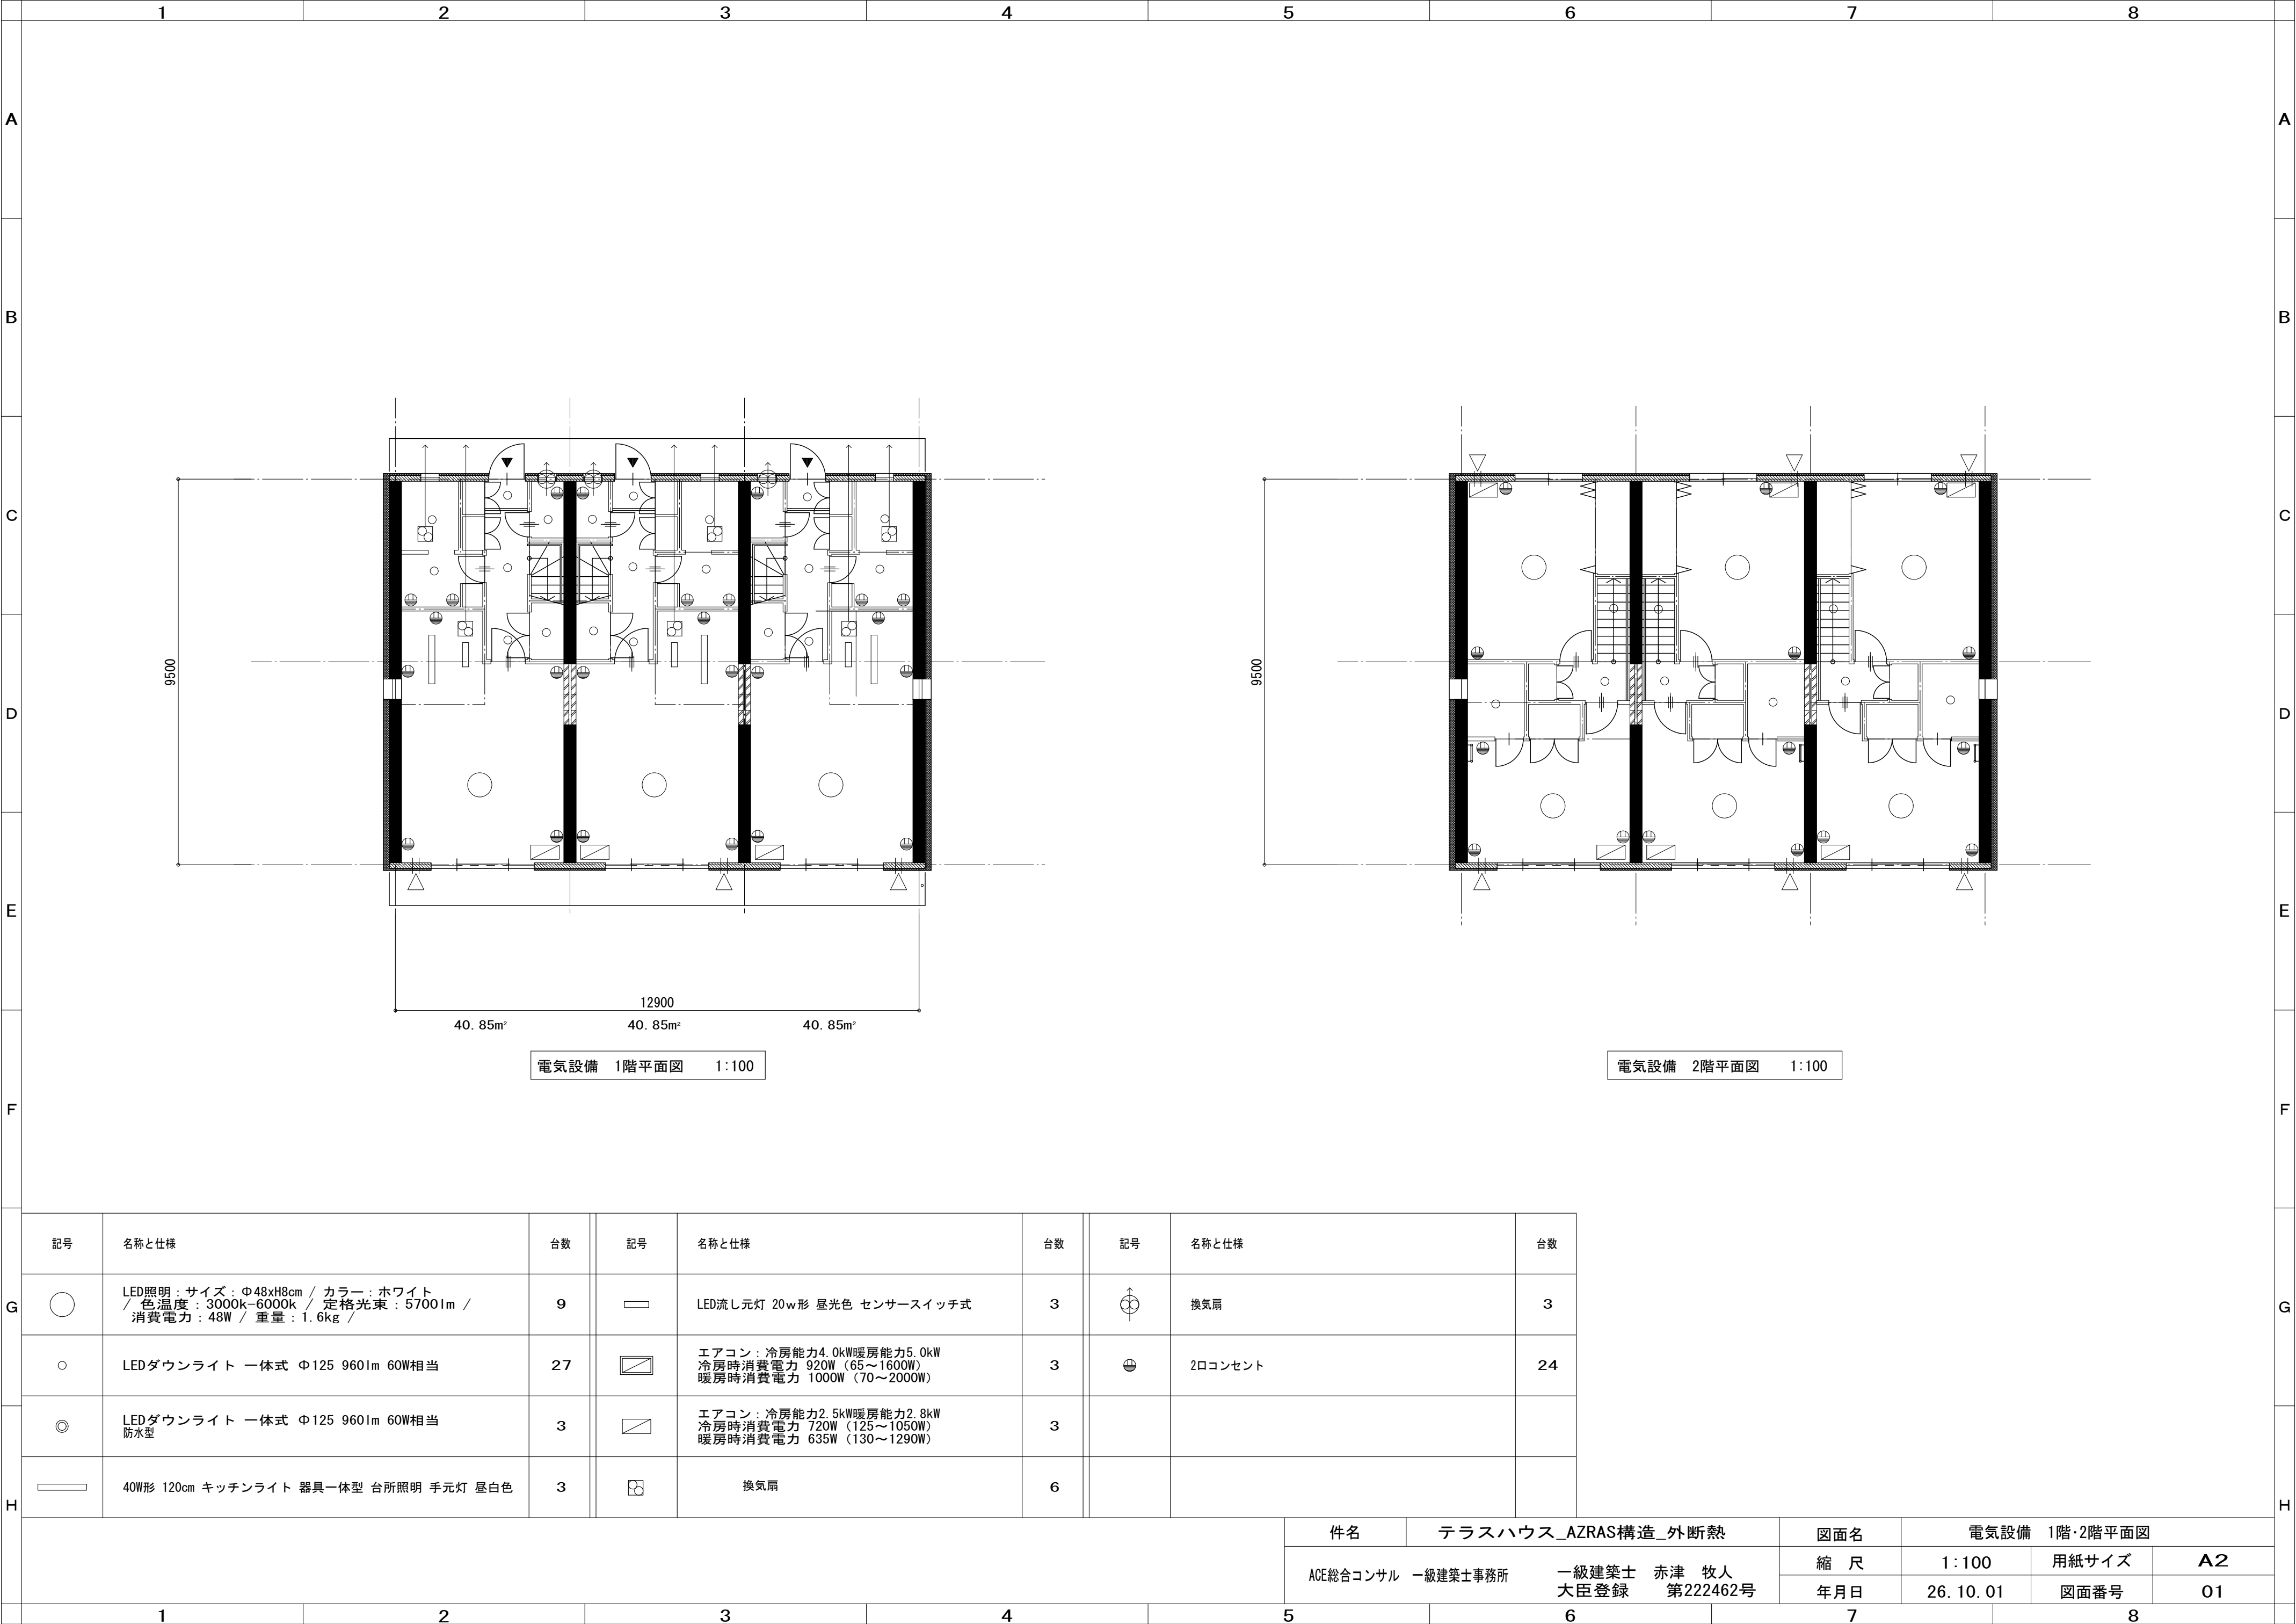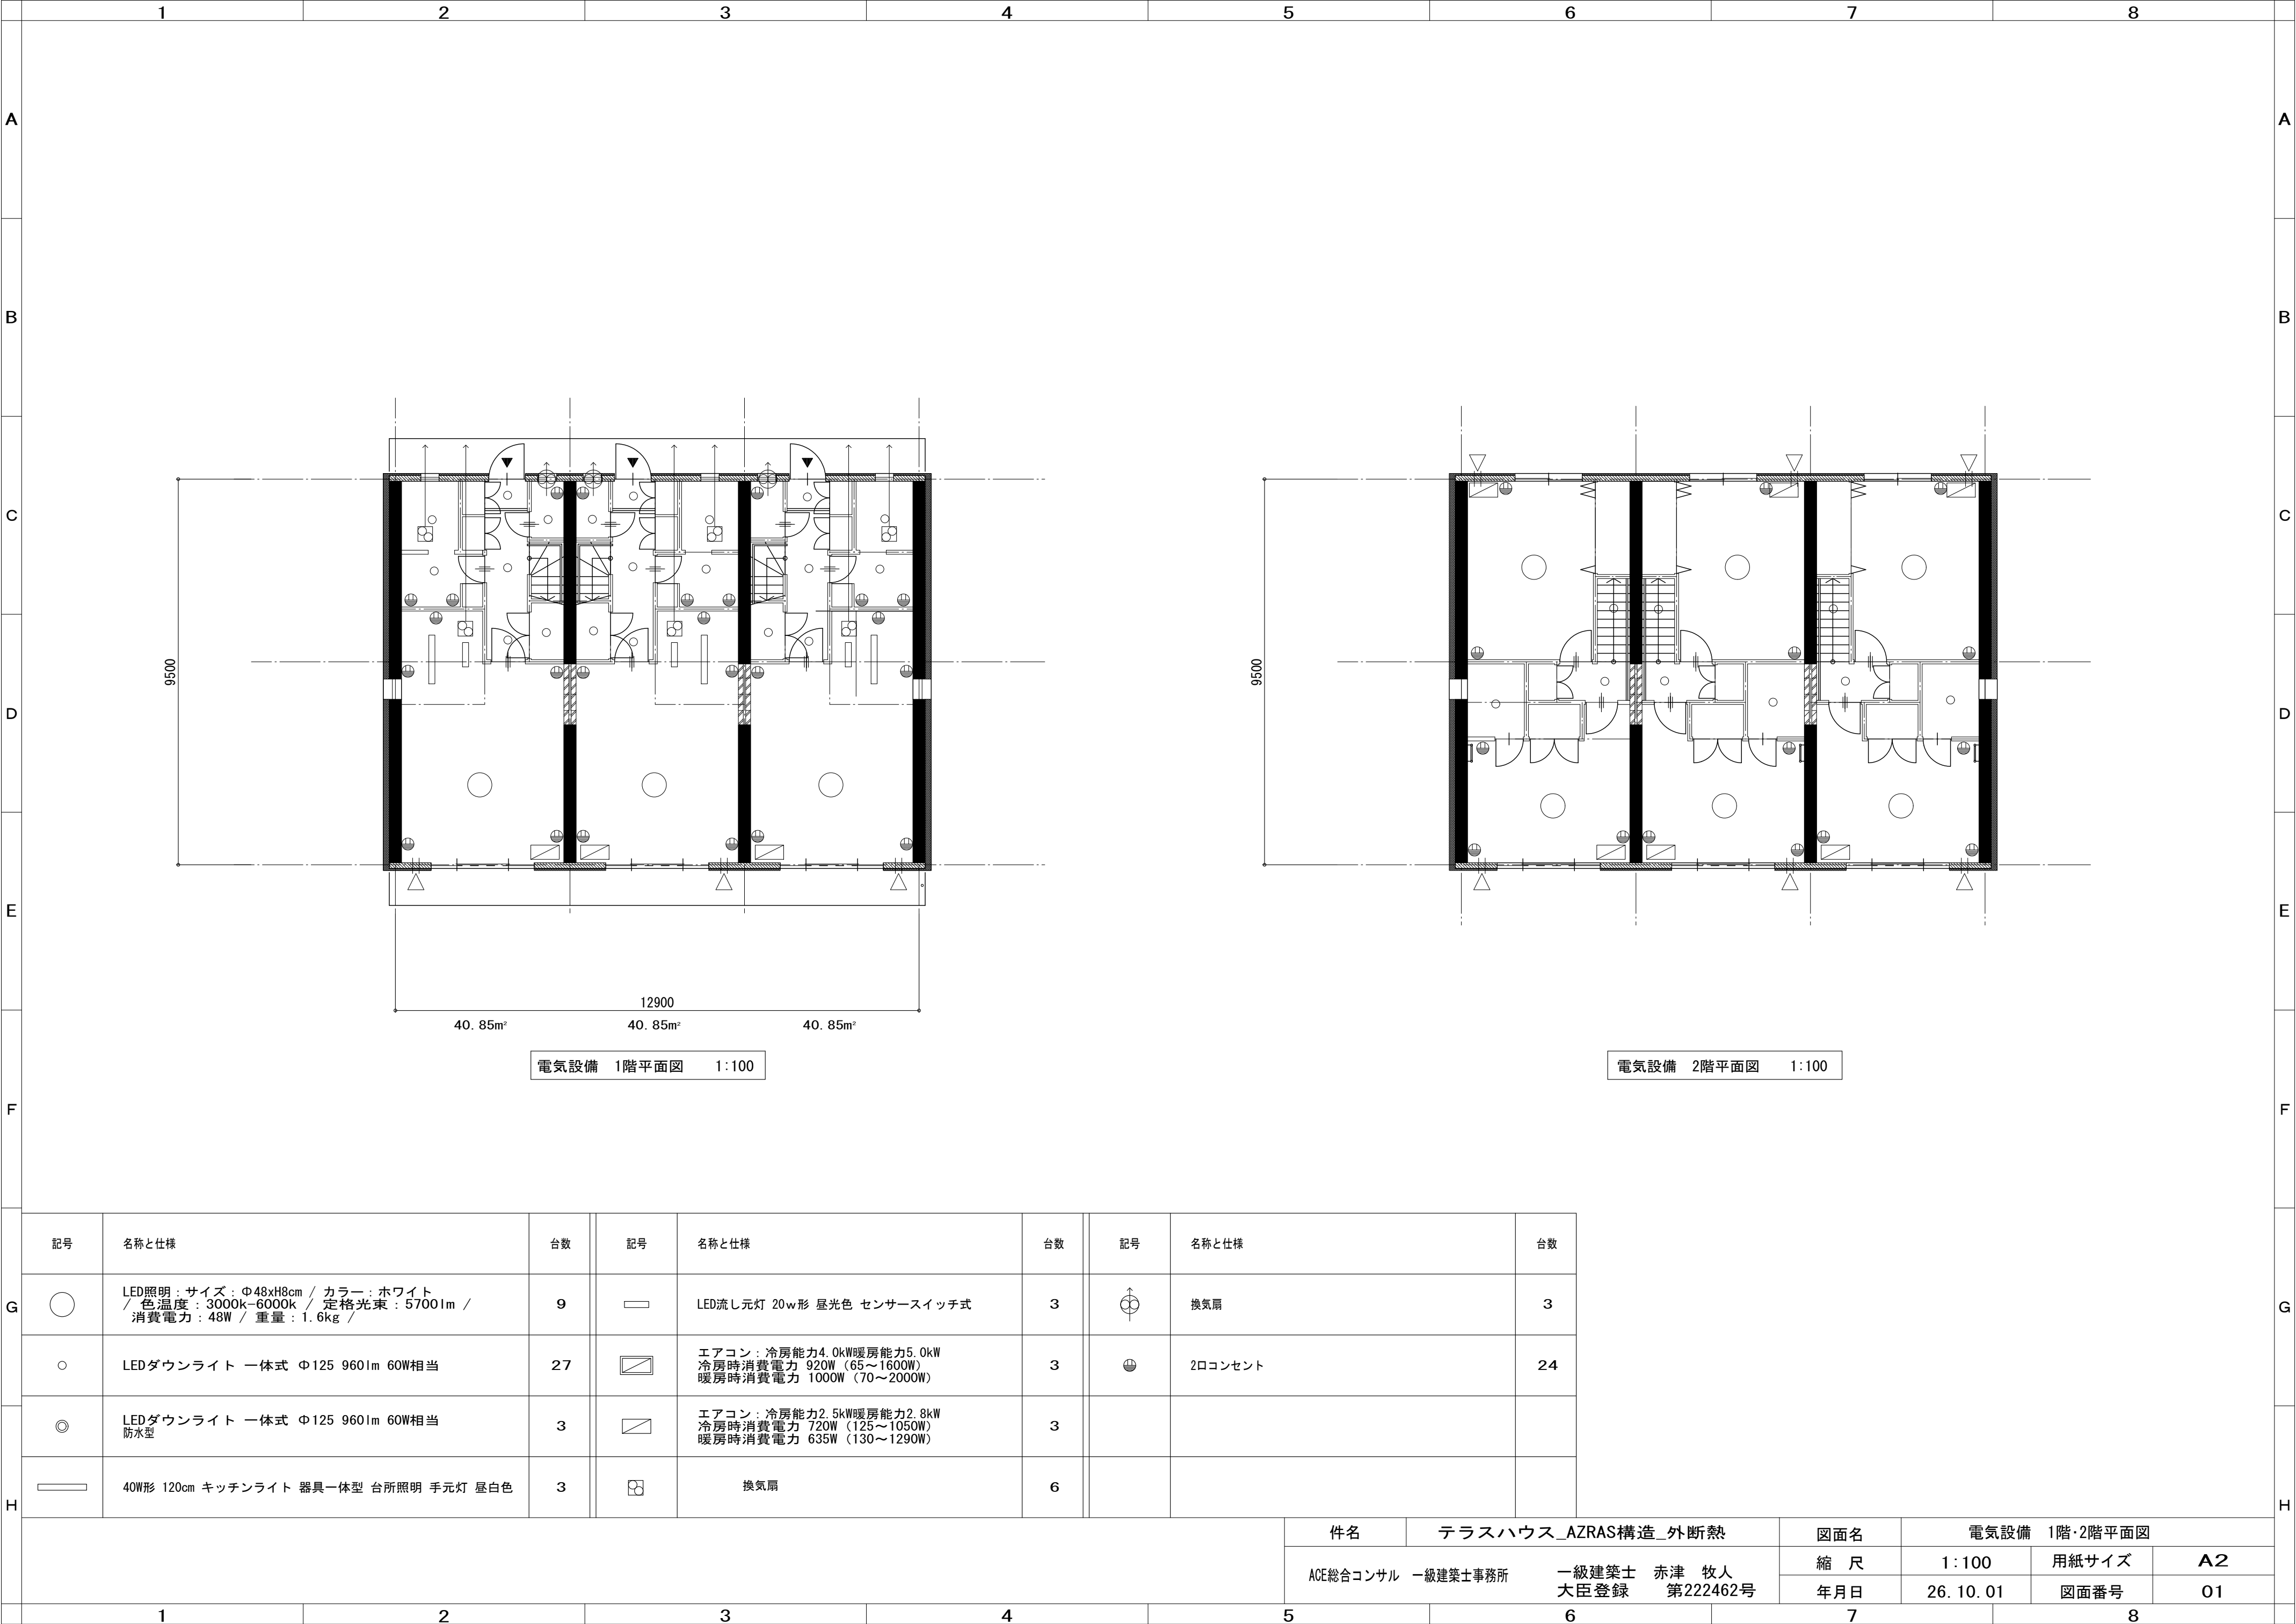

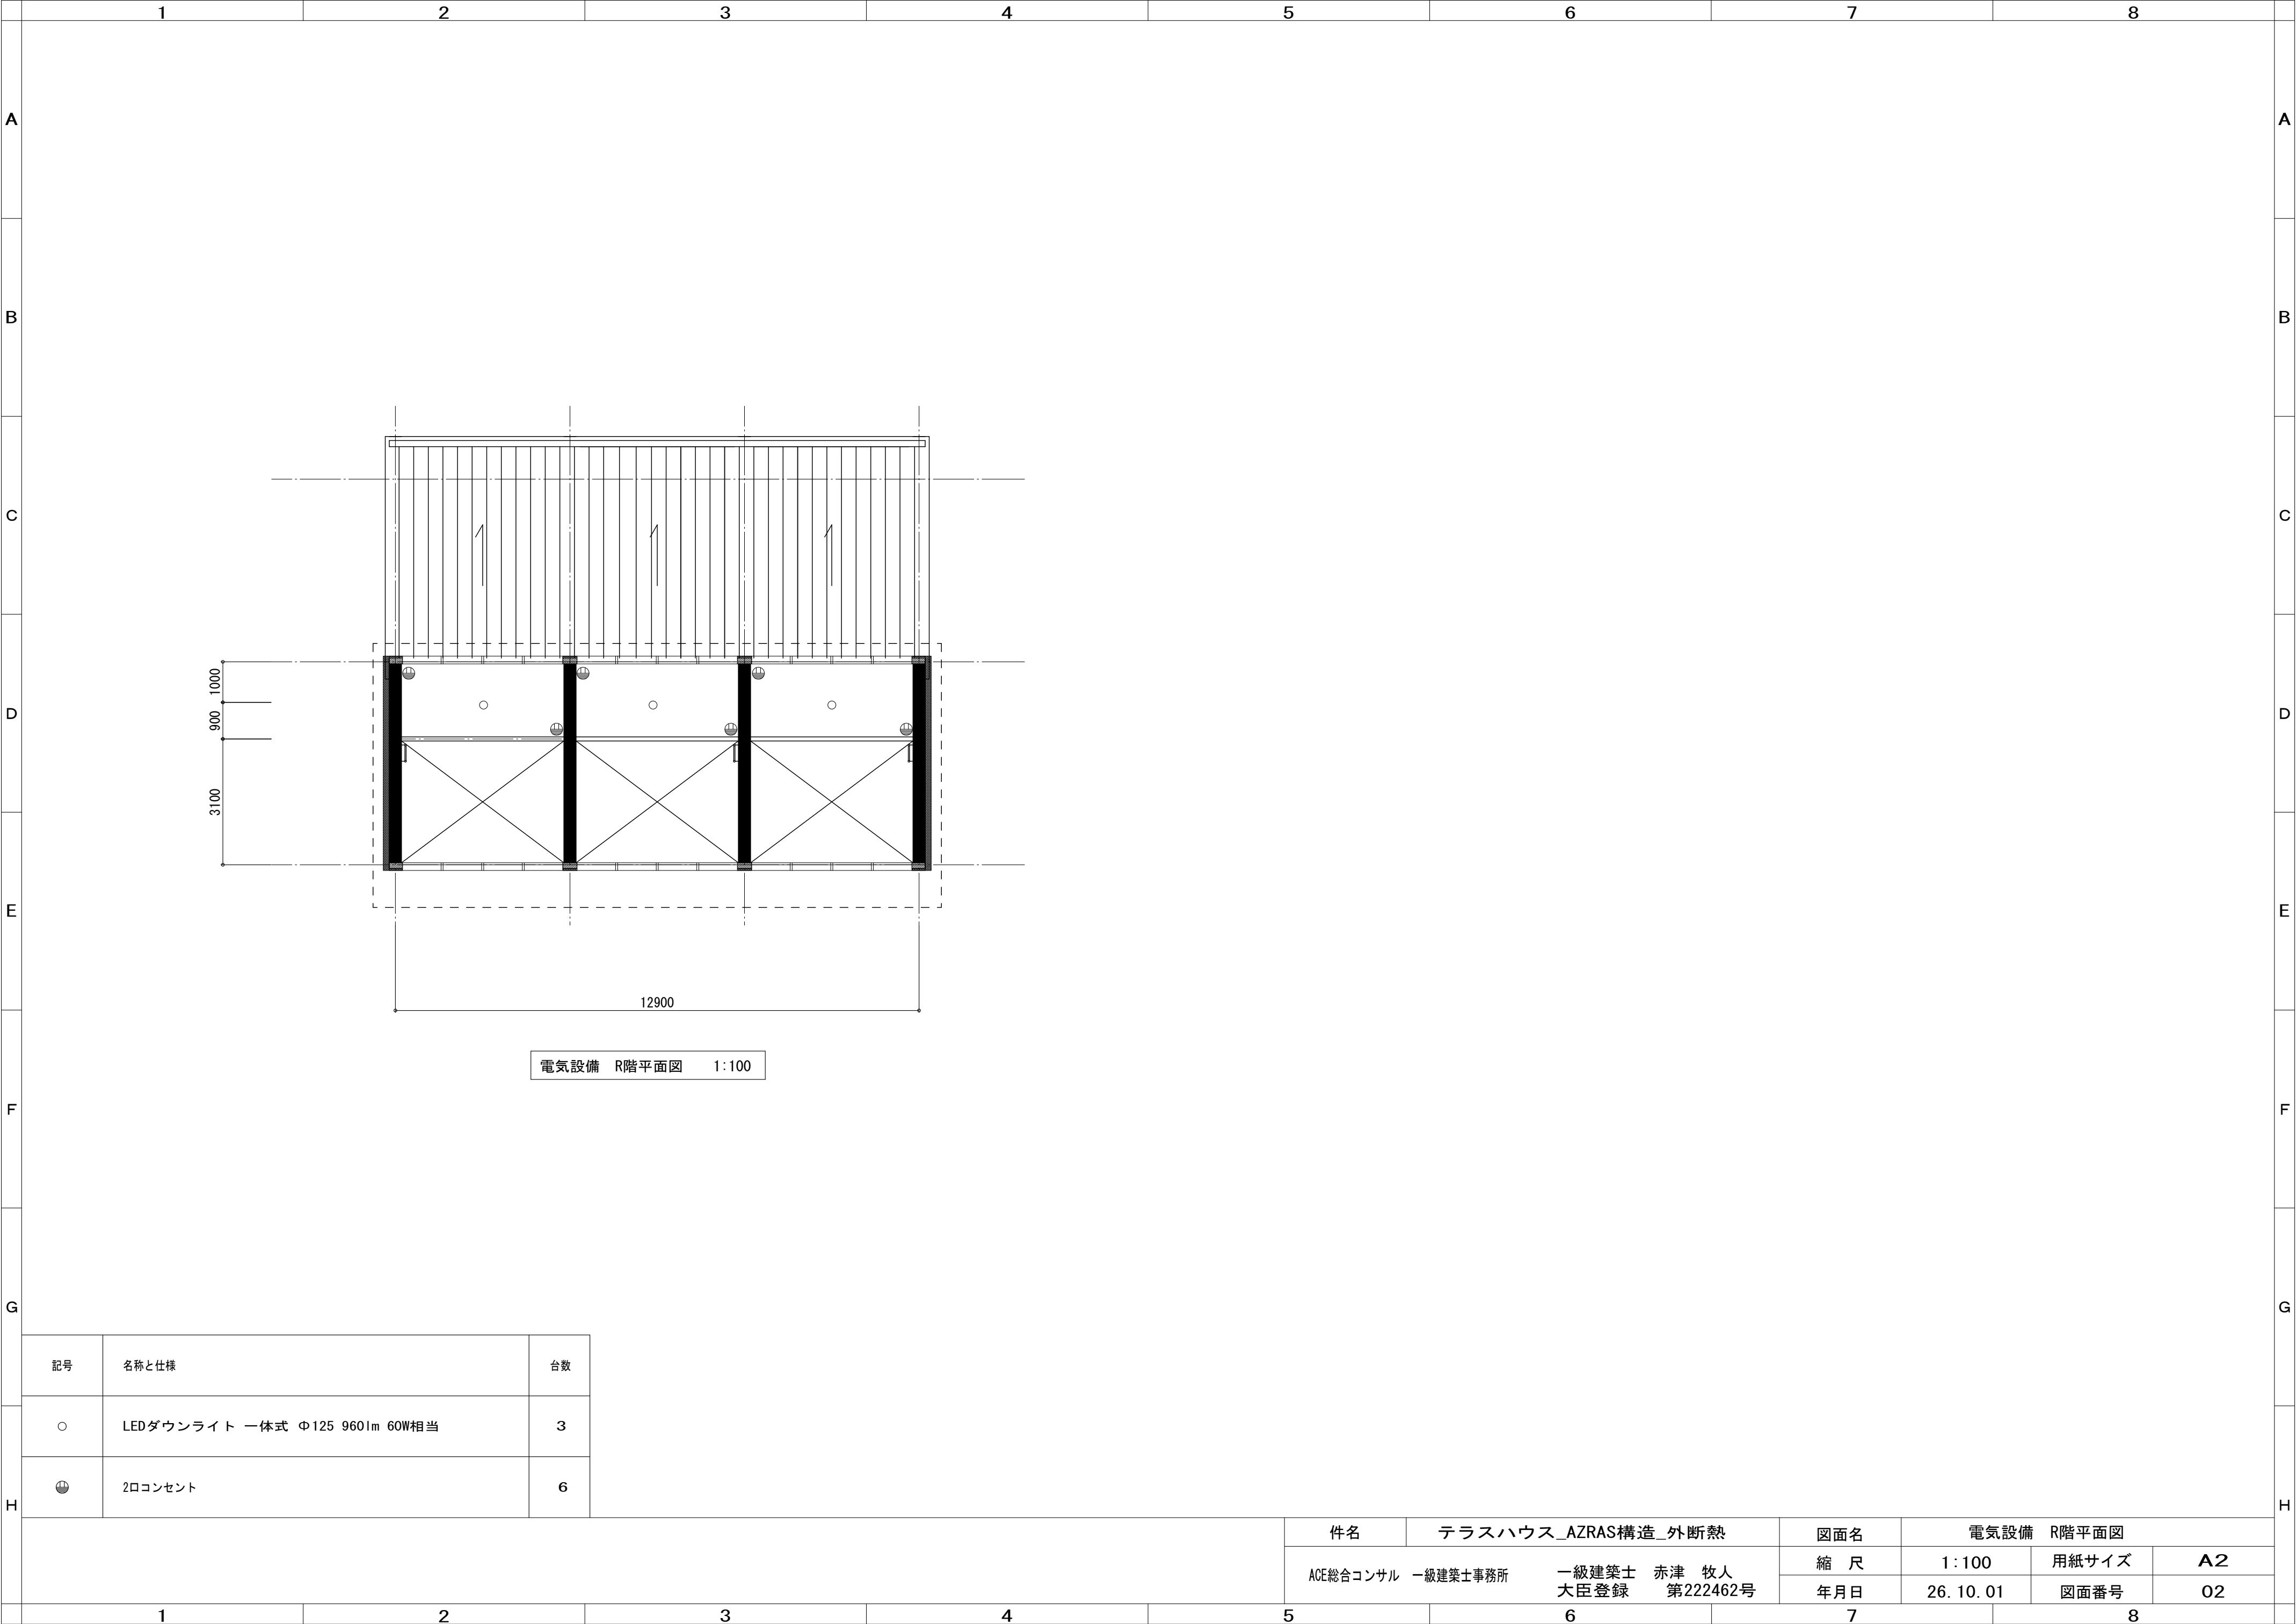

A

B

C

D

E

F

G

H

A

B

C

D

E

F

G

H