



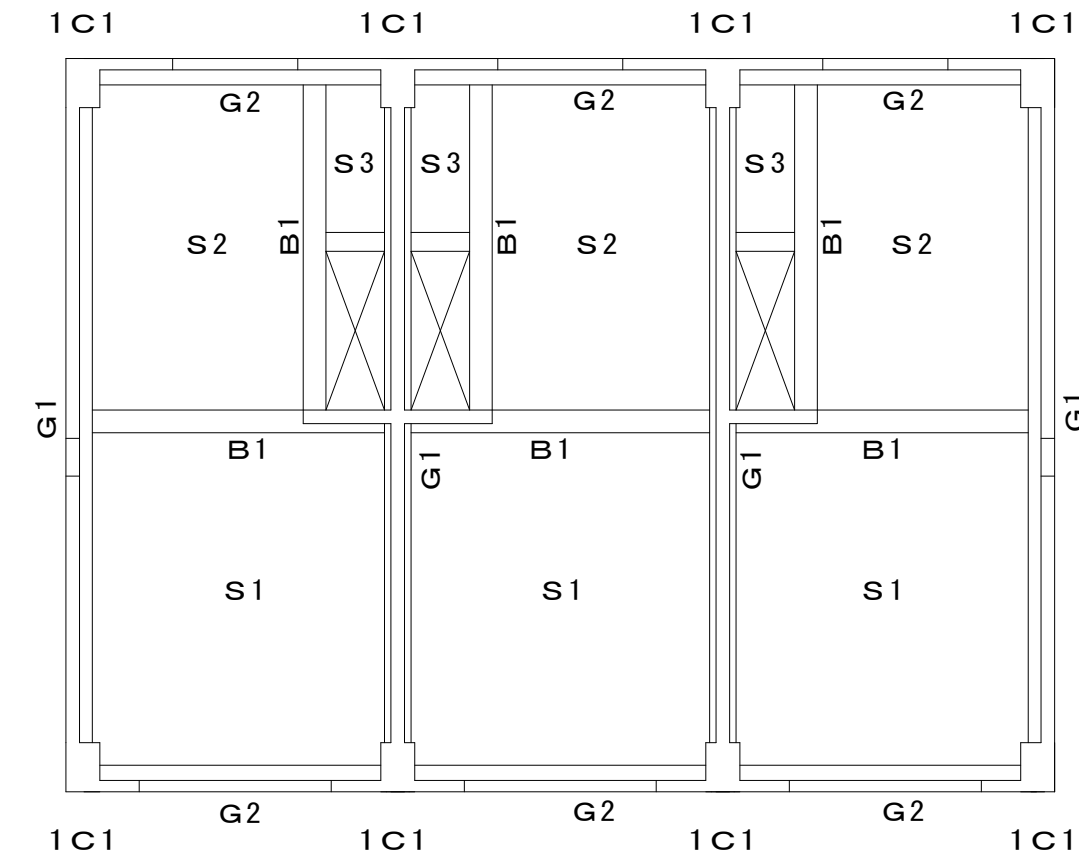


2階床伏せ見上図 1:100

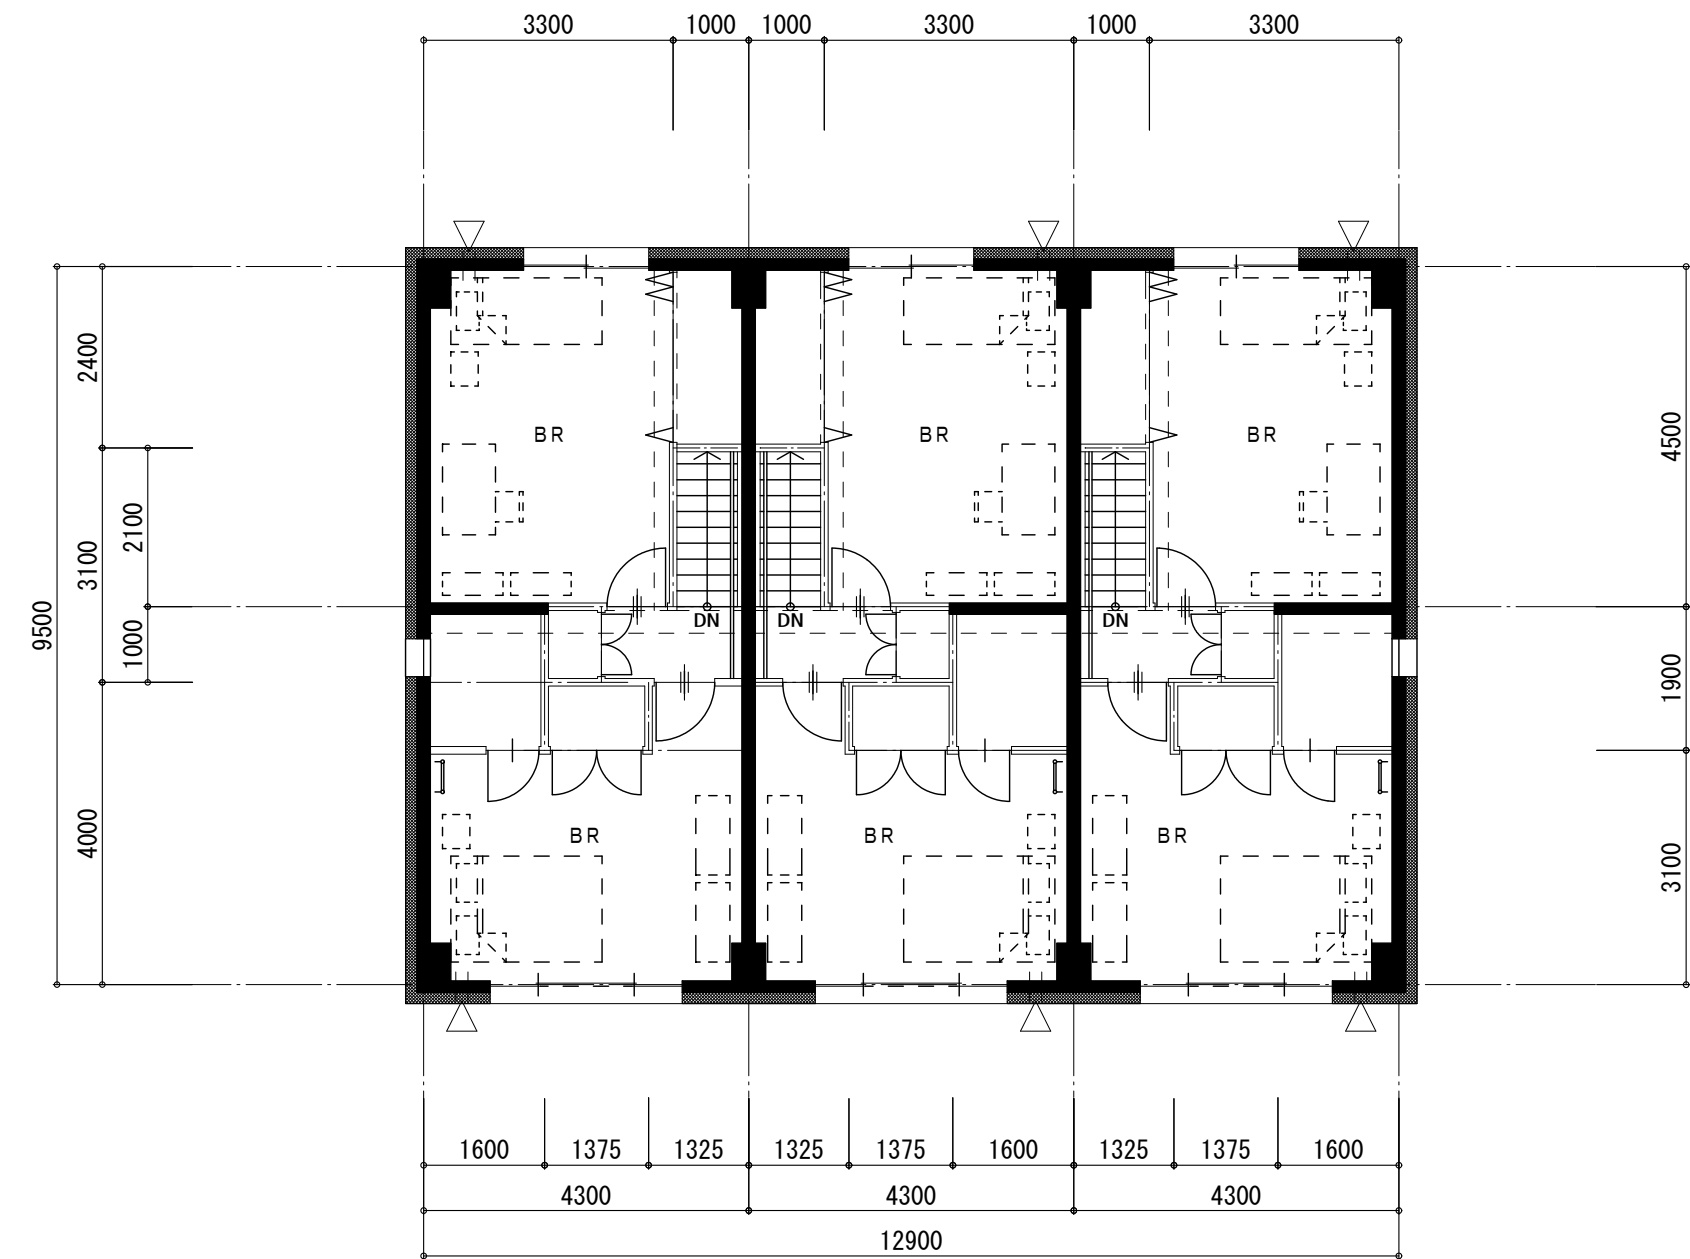


2階平面図 1:100


件名	テラスハウス_RCラーメン構造_外断熱			図面名	1階・2階平面図		
ACE総合コンサル 一級建築士事務所	一級建築士 赤津 牧人 大臣登録 第222462号	縮 尺	1:100	用紙サイズ	A2		
		年月日	26. 10. 01	図面番号	01		

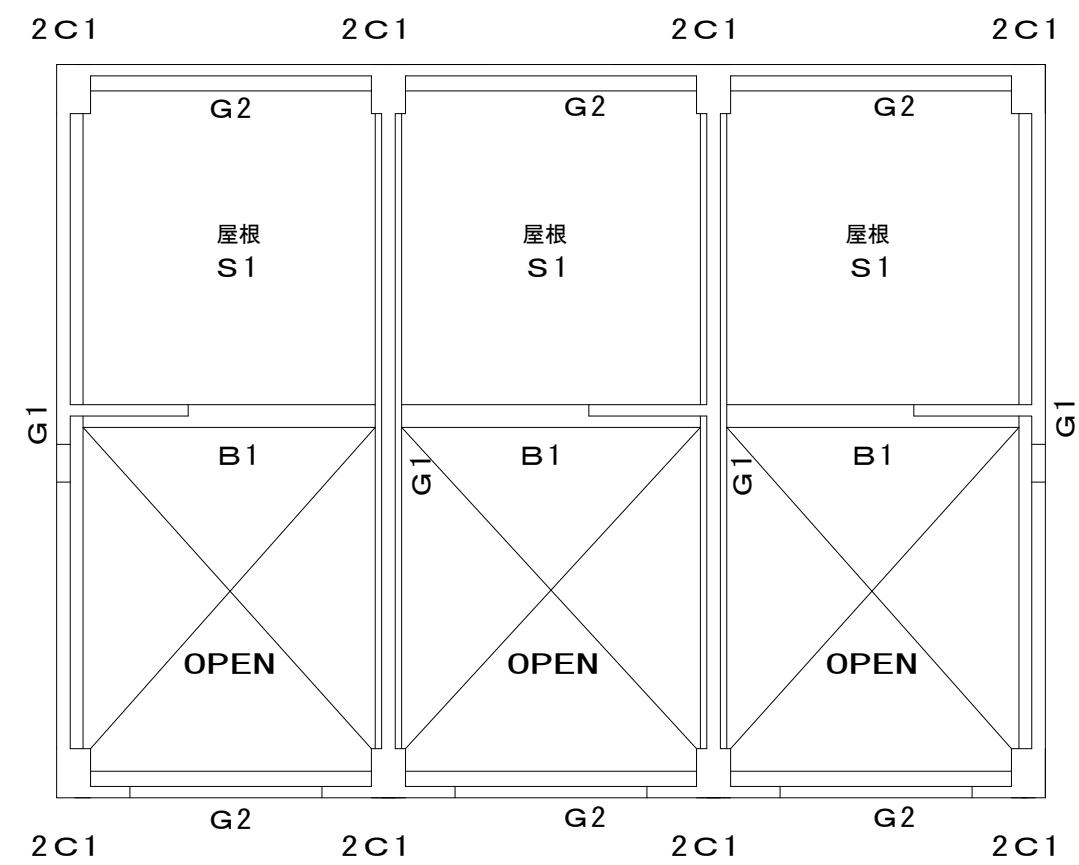


壁は全て厚さ150mm
S1は厚さ150mm
2 C1は全て600×450mm G1・G2・B1は全て350×500mmとする

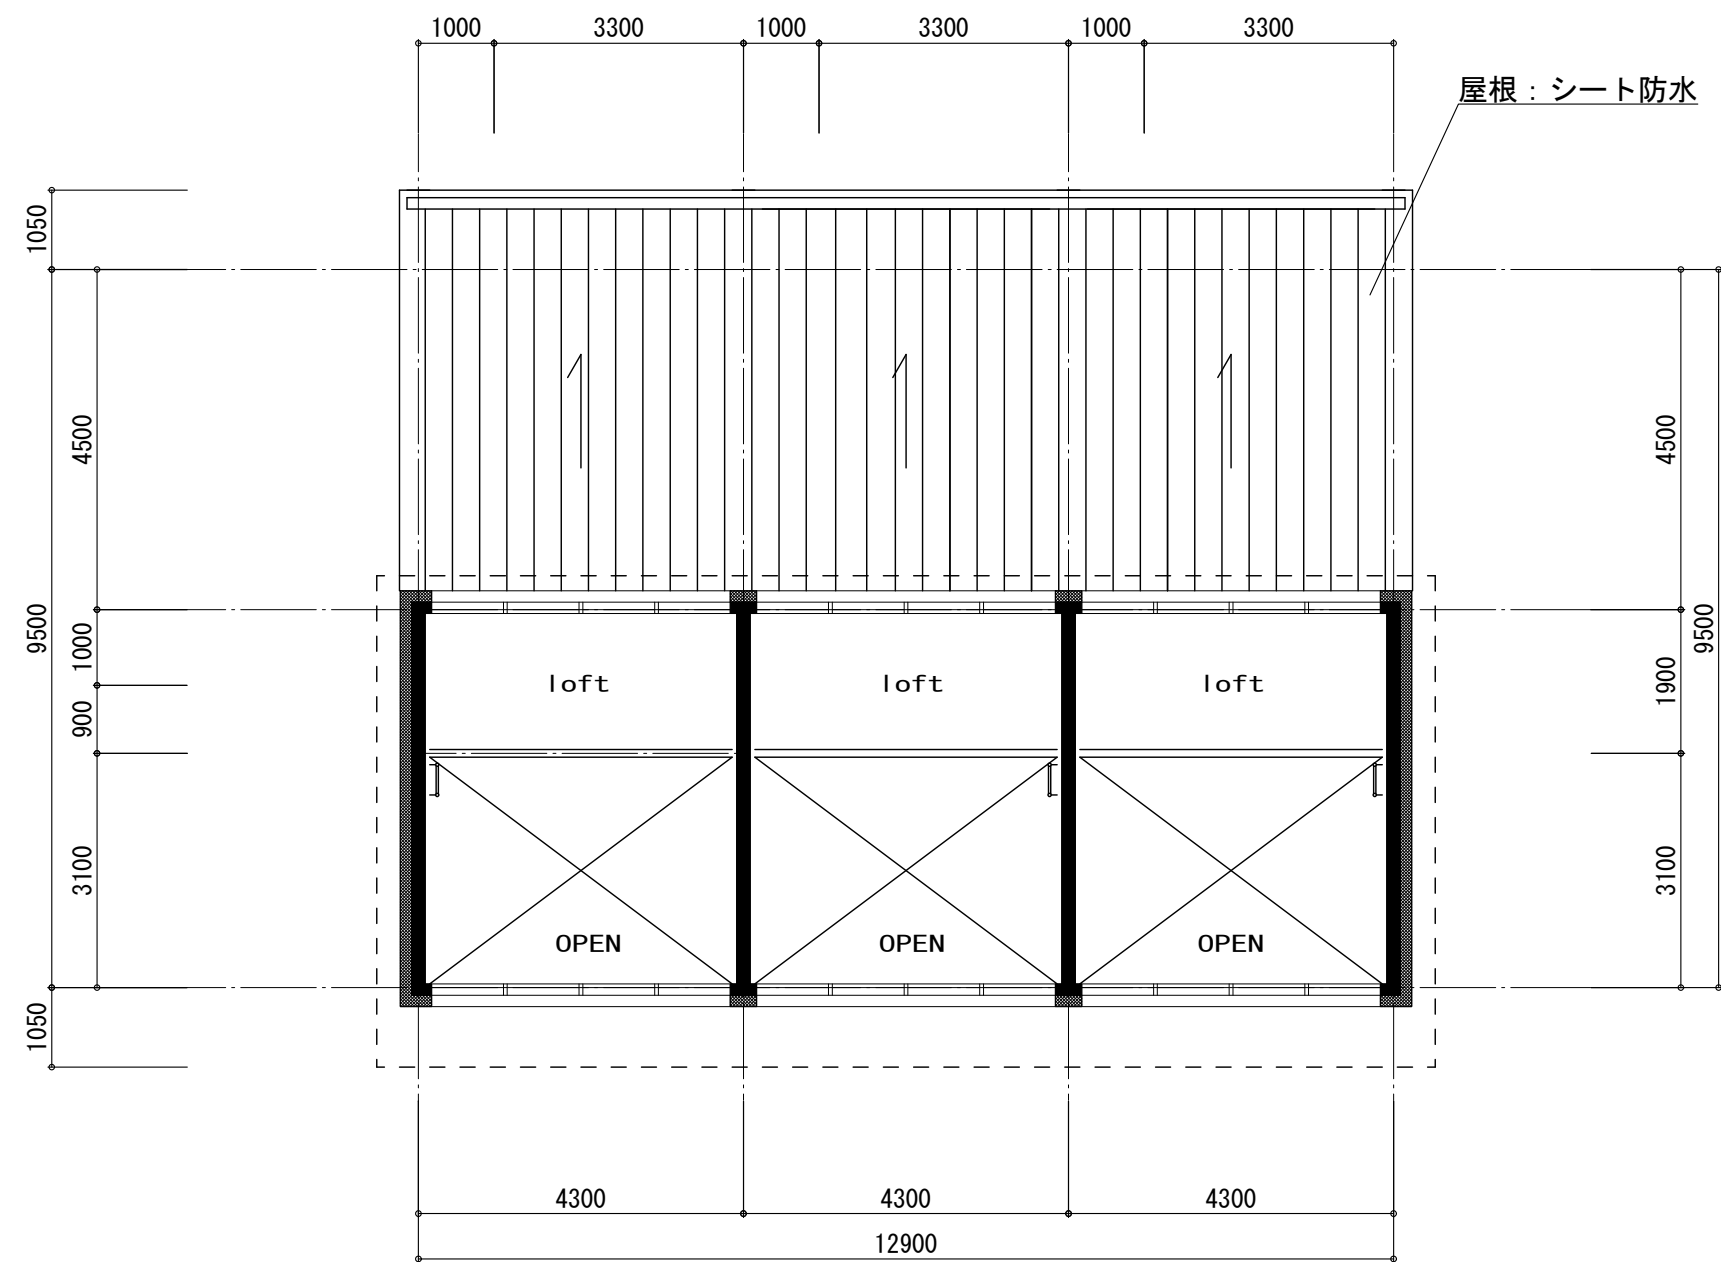

壁は全て厚さ150mm
S1は厚さ150mm

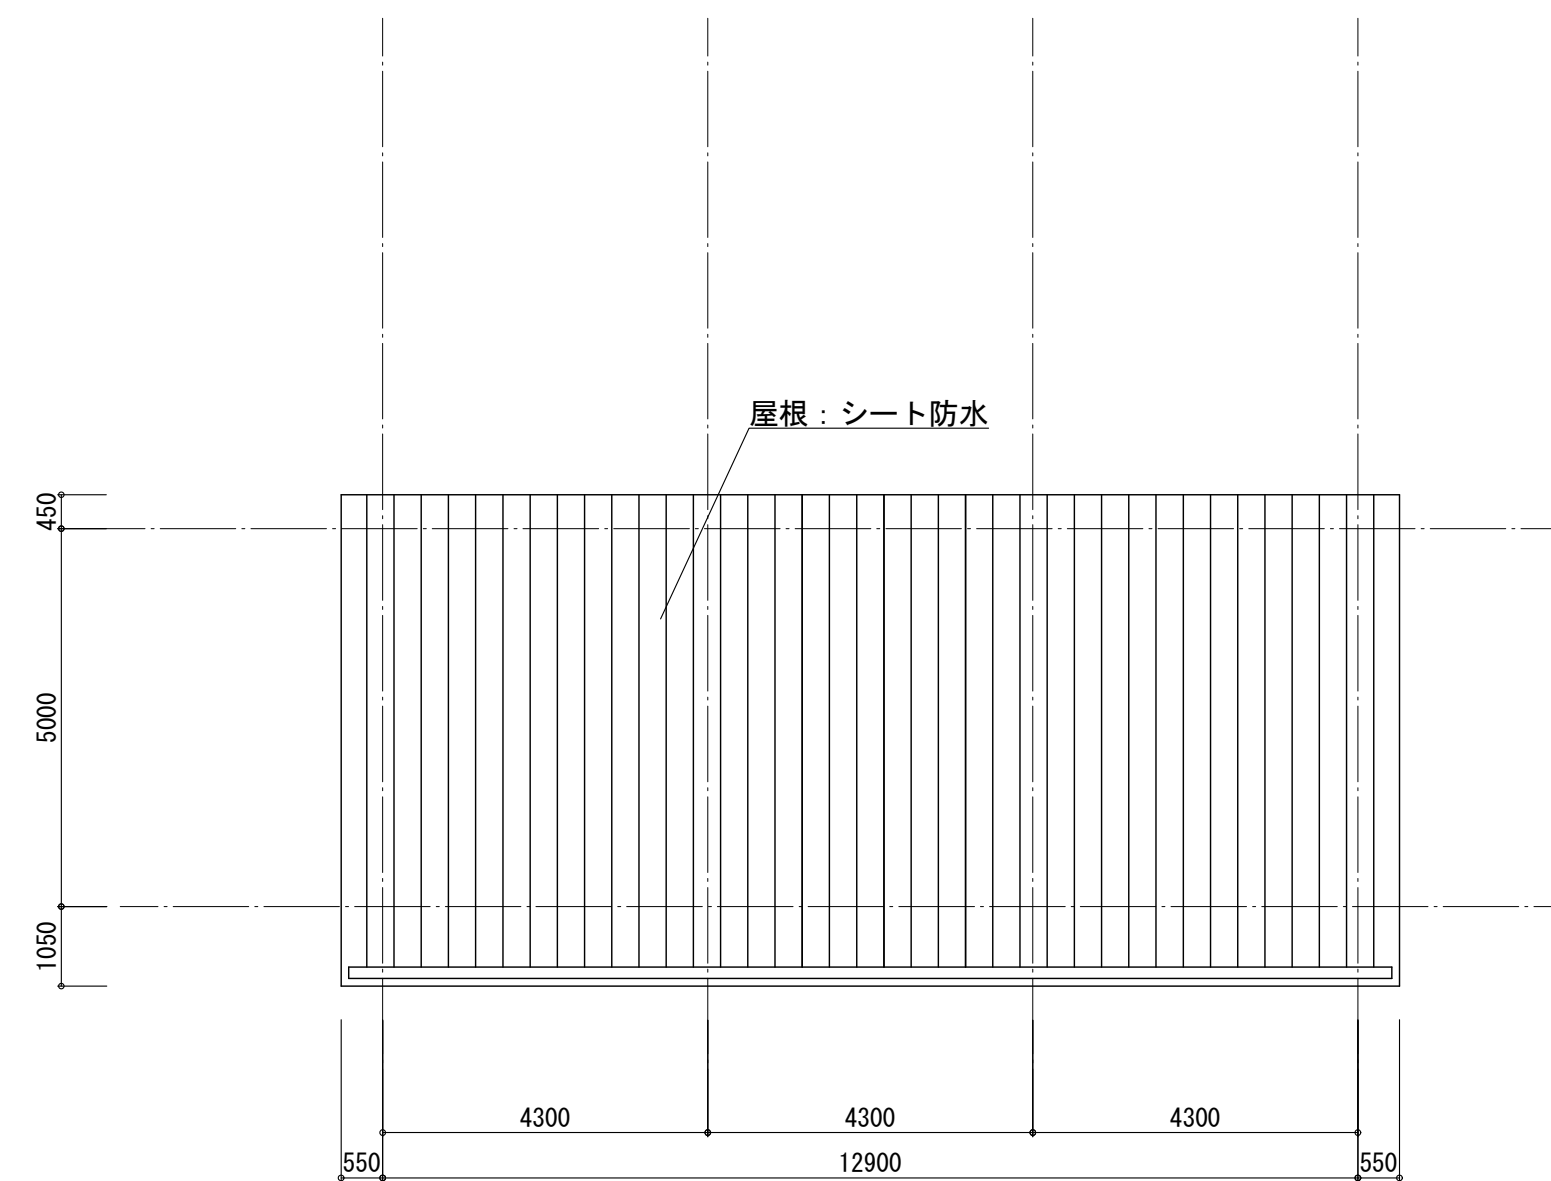

件名	テラスハウス_RCラーメン構造_外断熱			図面名	R階平面図・屋根伏図		
ACE総合コンサル 一級建築士事務所 大臣登録 赤津 牧人 第222462号				縮 尺	1:100	用紙サイズ	A2
				年月日	26. 10. 01	図面番号	02

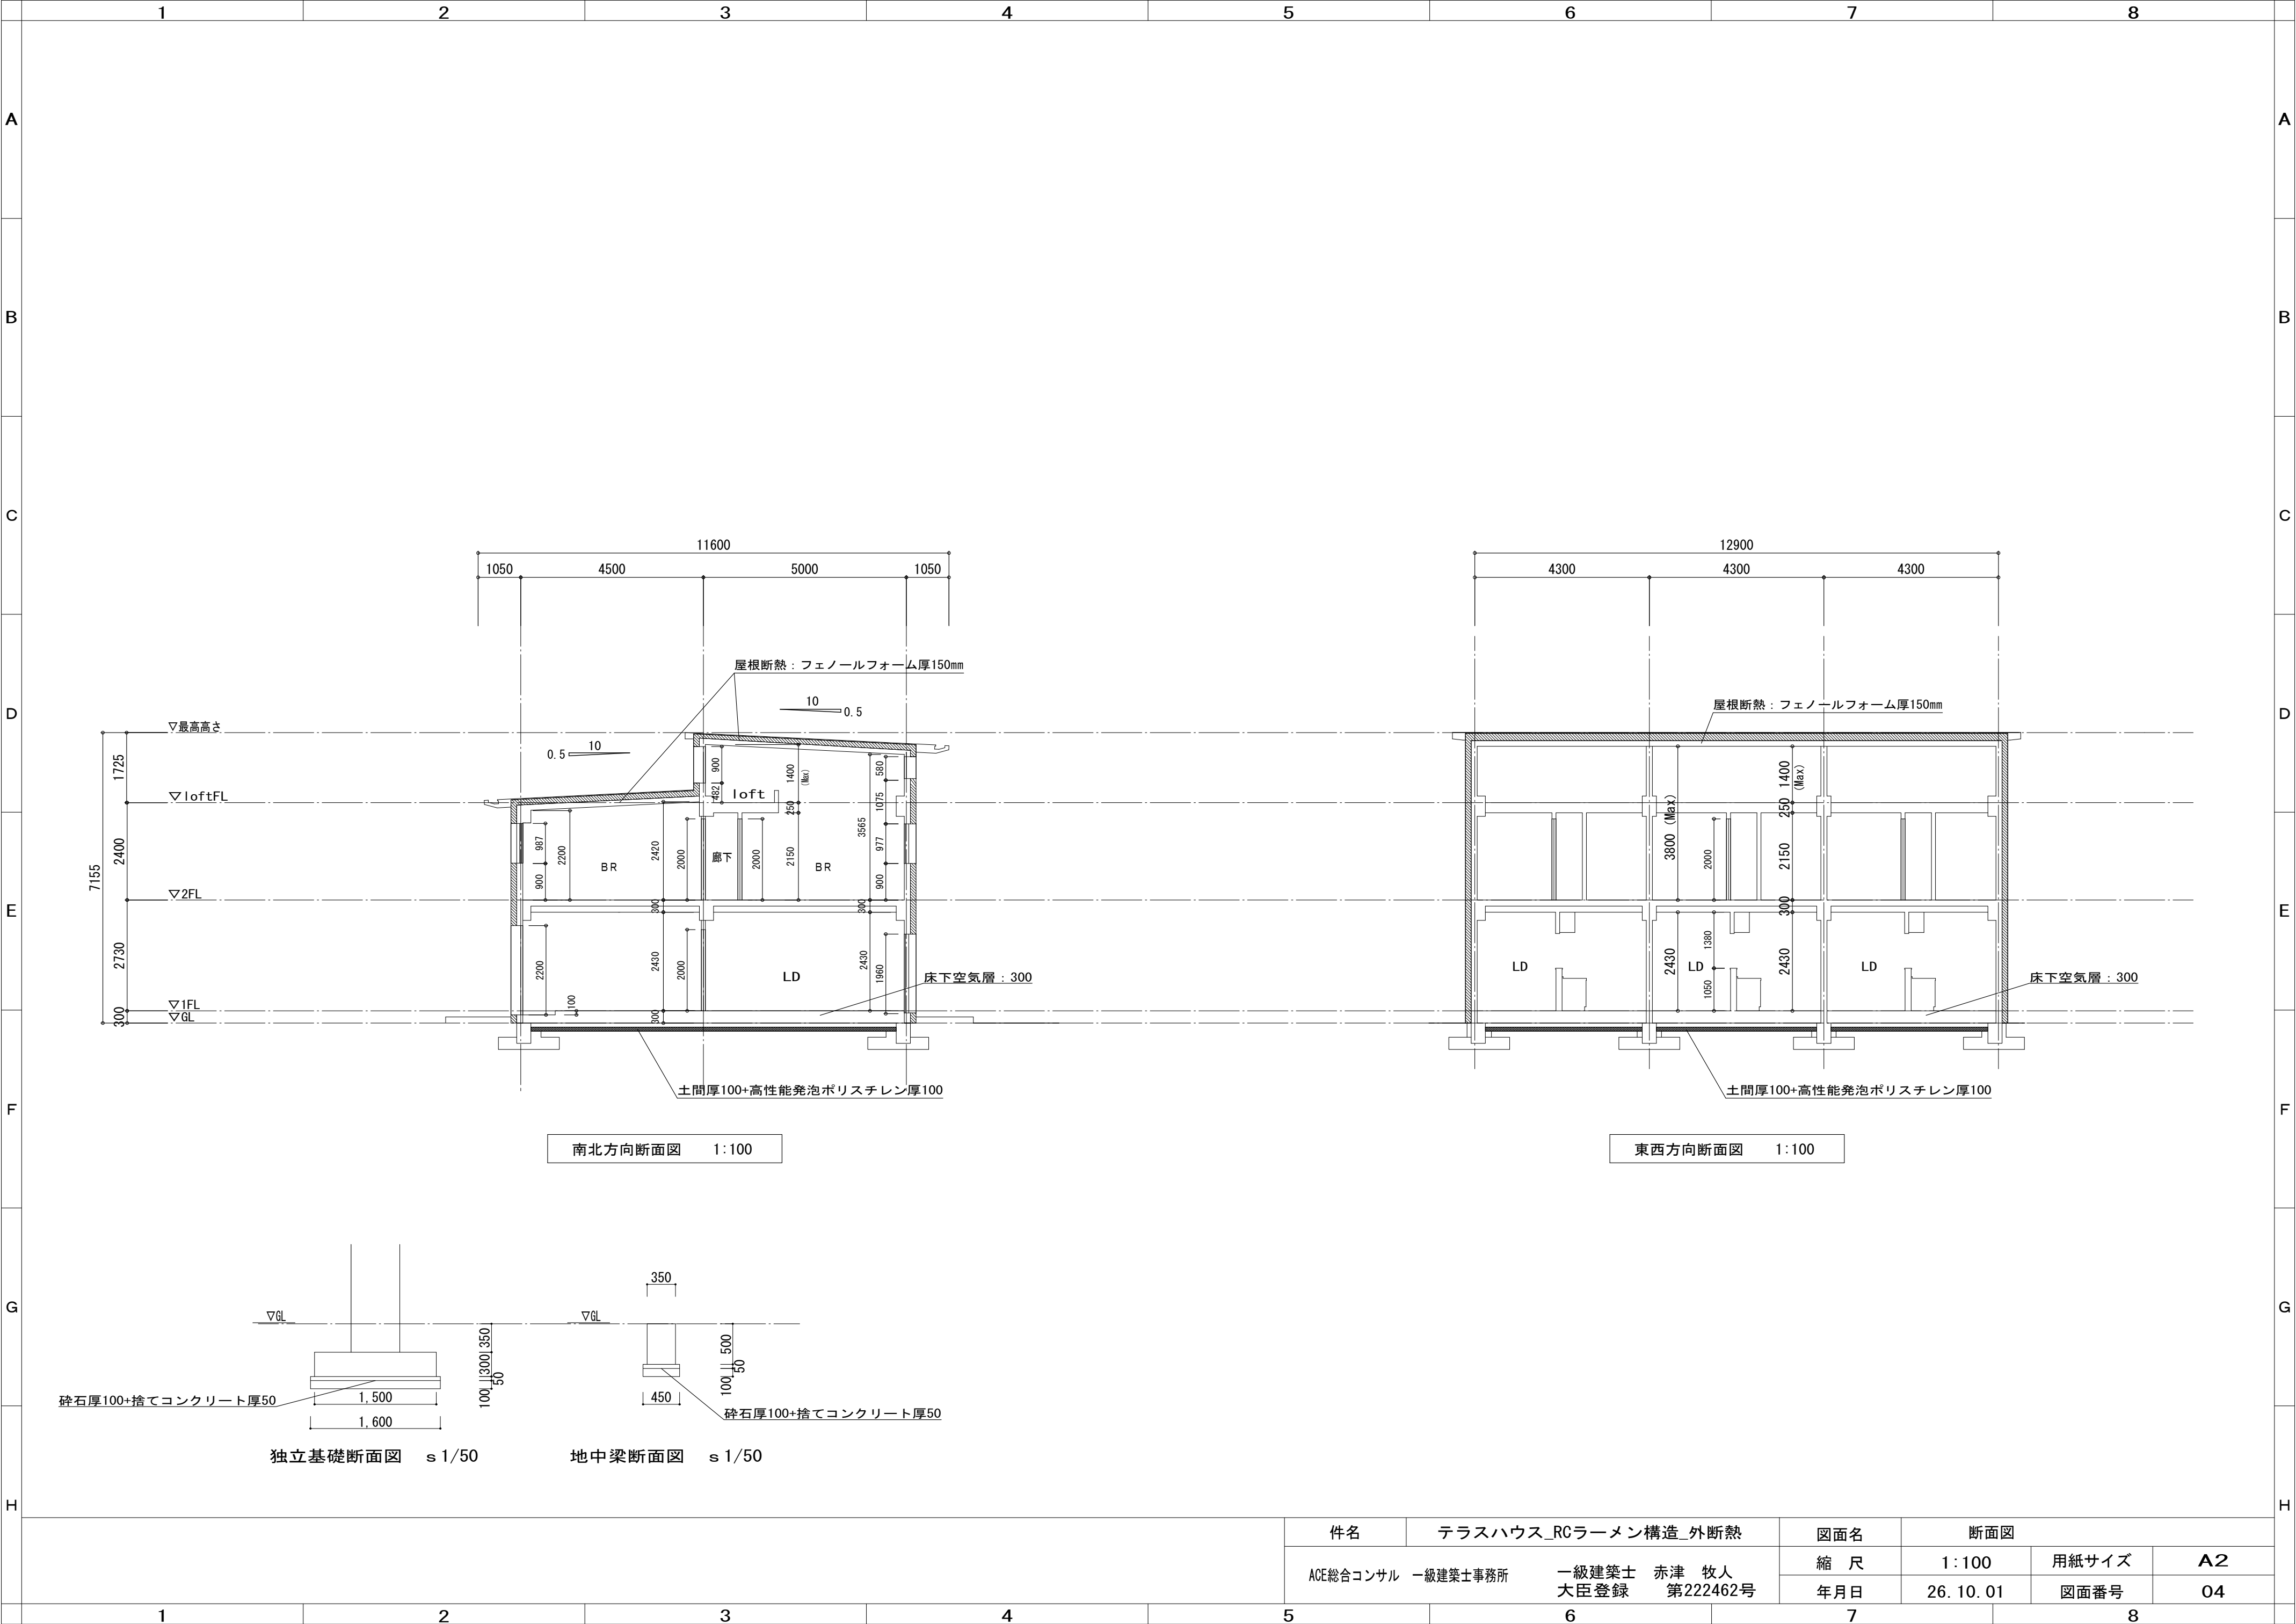

					件名	テラスハウス_RCラーメン構造_外断熱	図面名	断面図		
					ACE総合コンサル 一級建築士事務所	一級建築士 赤津 牧人 大臣登録 第222462号	縮 尺	1:100	用紙サイズ	A2
							年月日	26. 10. 01	図面番号	04
1	2	3	4	5	6	7	8			

